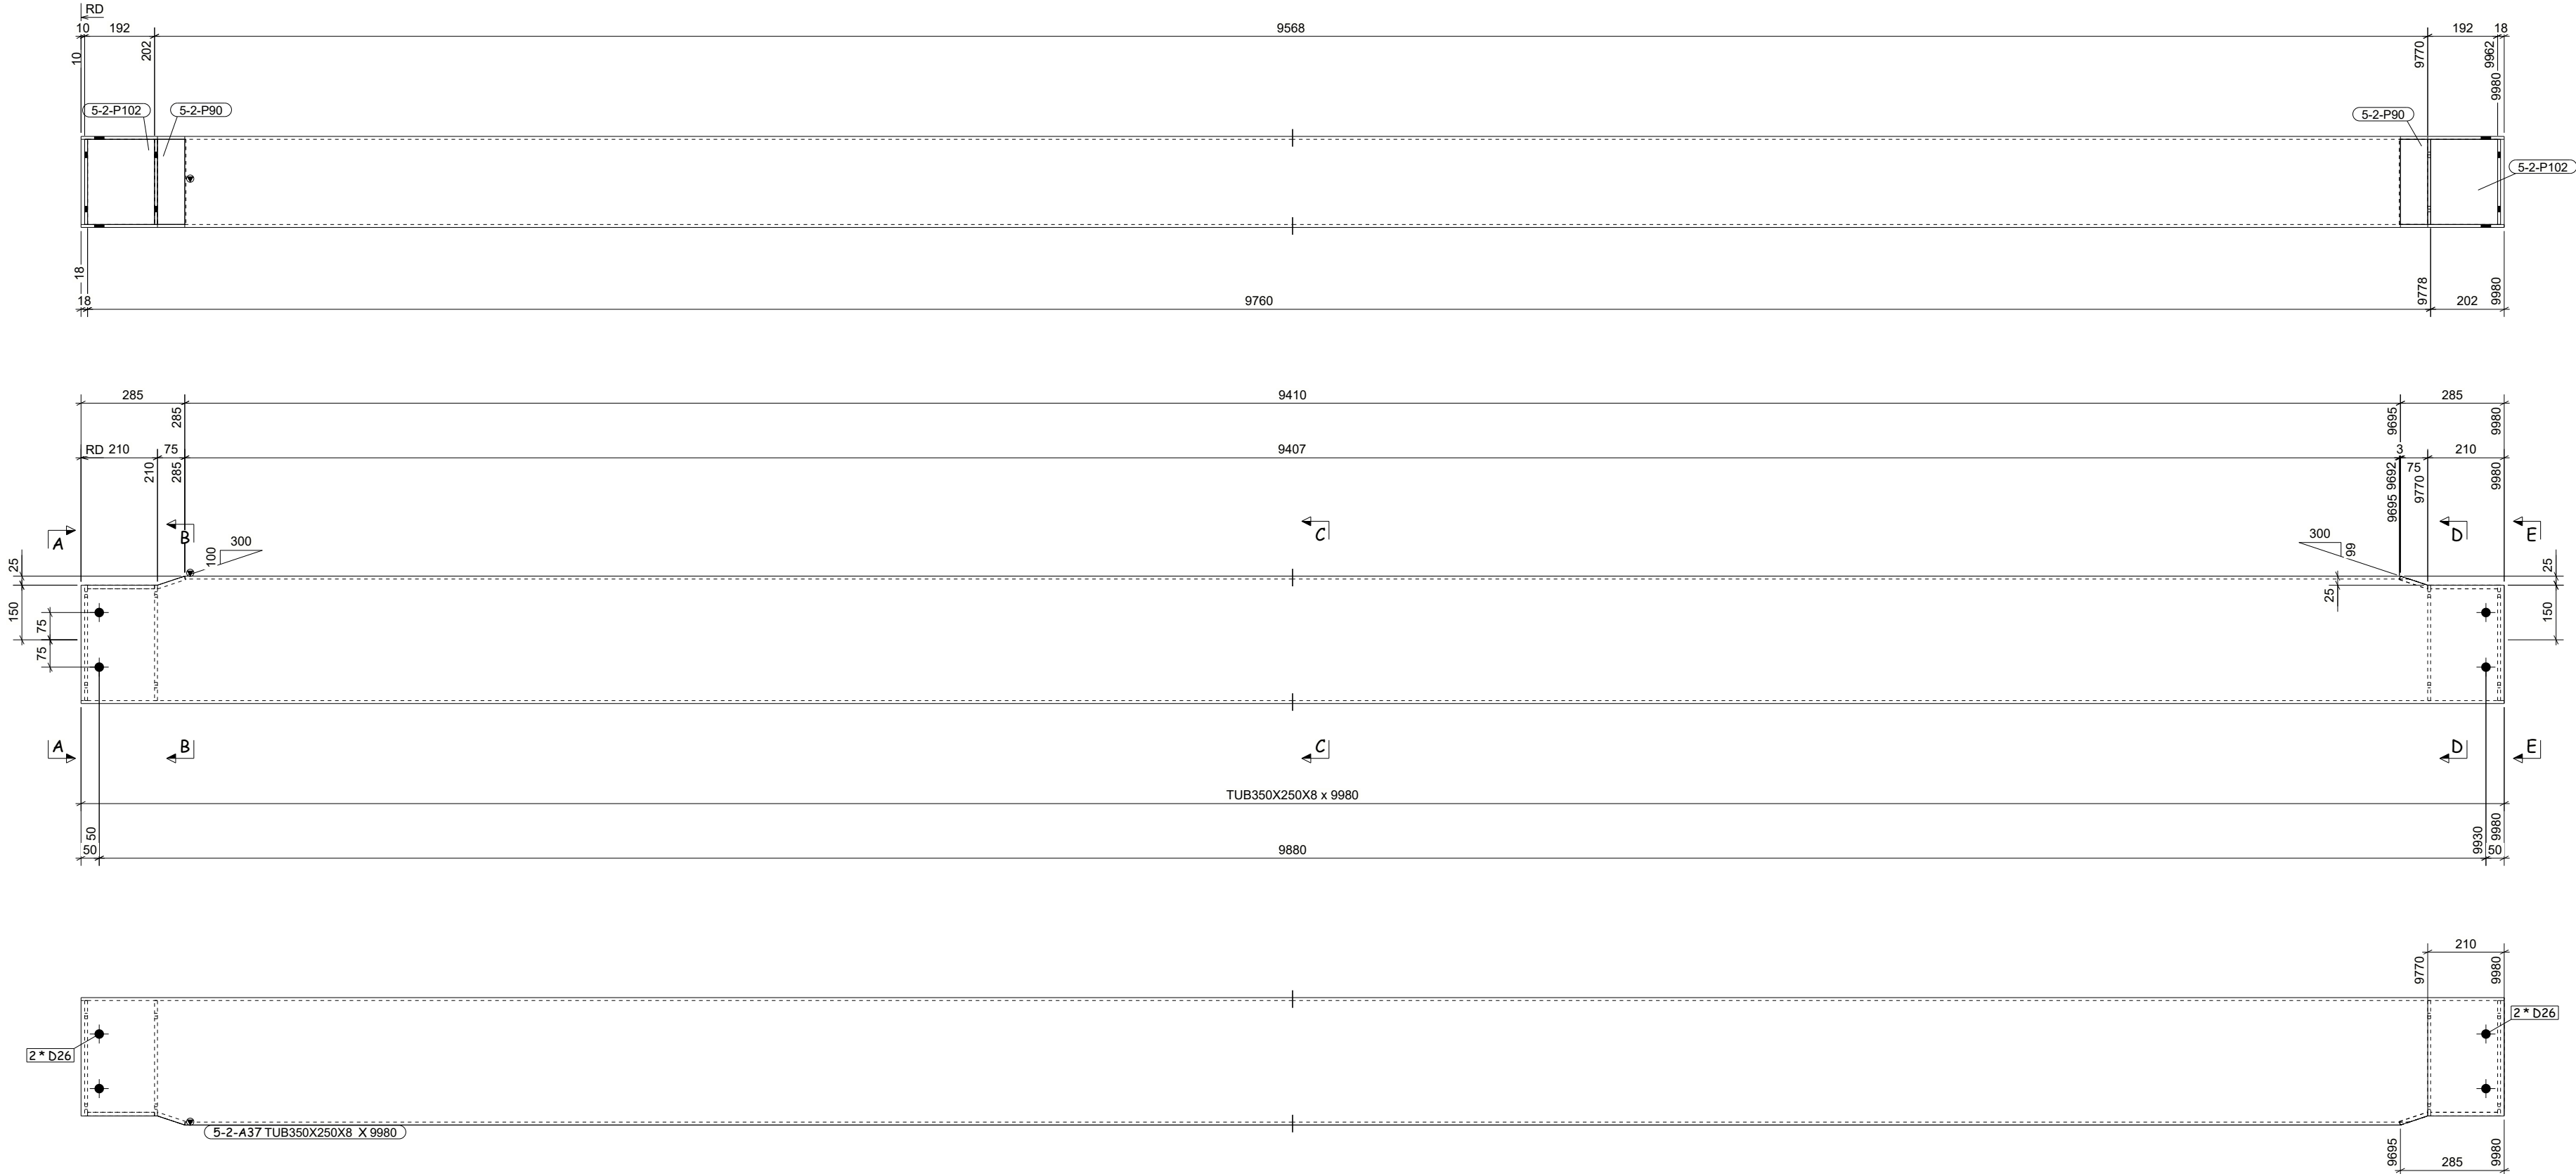


DRAWING NO. : 1μÚŋpÁú-5-2-A37										REV.:									
ERECTION MARK : 1μÚŋpÁú-5-2-A37										DESCRIPTION : BEAM									
HOLD : TYPE : TREAT : COST CODE : REMARKS :										QTY : 1 NOS									
LENGTH : 9980										WIDTH : 250									
HEIGHT : 350										TOTAL S.AREA : 12.7 (M2)									
POS NO.	QTY PER ASSLY	SECTION		LENGTH	UNIT WEIGHT (Kg)	TOTAL QTY	WEIGHT	GRADE	REVISION	PART ID	TREATMENT	ABRN ID	TOP F.S.S. ABRN ID	PARTIAL S.A ABRN ID	MULTIPLY CC ABRN ID	SWI NO	REMARKS		
5-2-P4	1	TUB350X250X8		9980	732.049	1	732.049	S275		MM									
5-2-P78	4	PL8*234		317	4.660	4	18.637	S275		WI									
5-2-P90	2	PL10*82.4		234	1.512	2	3.024	S275		WI									
5-2-P102	2	PL10*184.2		234	3.383	2	6.763	S275		WI									
					UNIT WEIGHT :-		760.47												
					TOTAL WEIGHT :-		760.47												

1 NO. BEAM MKD' 1μÚŋpÁú-5-2-A37

REV	DATE	DESCRIPTION	DRAWN	CHK'D	APPD.
BUIL'D DESC.		Tekla Corporation			
PROJECT					
CUSTOMER					
SITE LOCATION					
JOB NO.		1μÚŋpÁú	CAD FILES:		
DRAWING TITLE:		BEAM SHEET 0		DRAWING NO. :	
				1μÚŋpÁú-5-2-A37	