
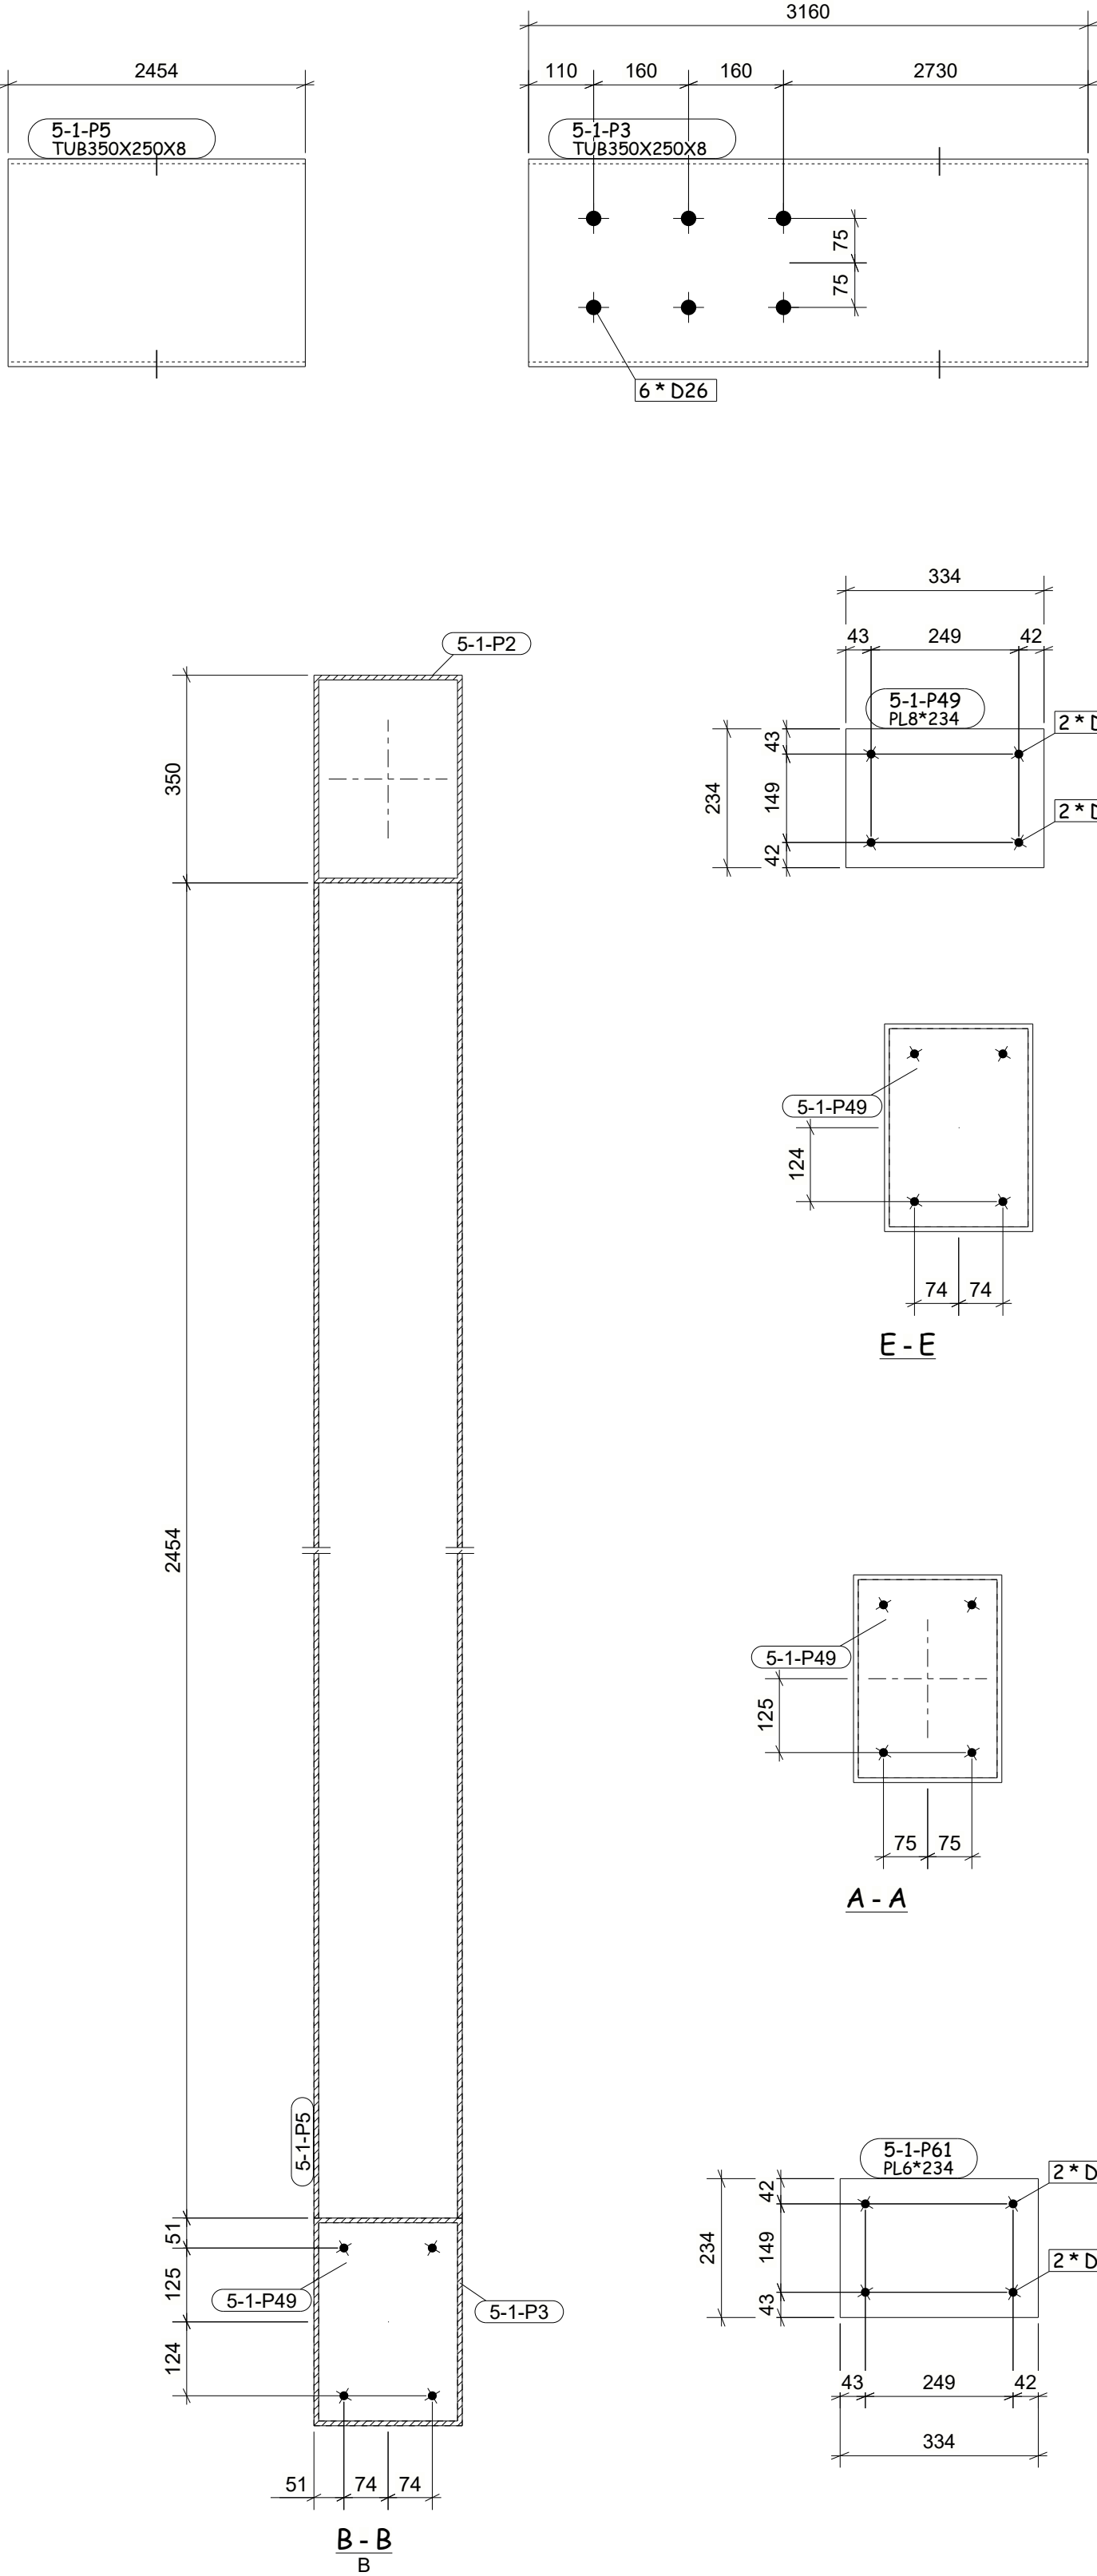


Tekla Structures

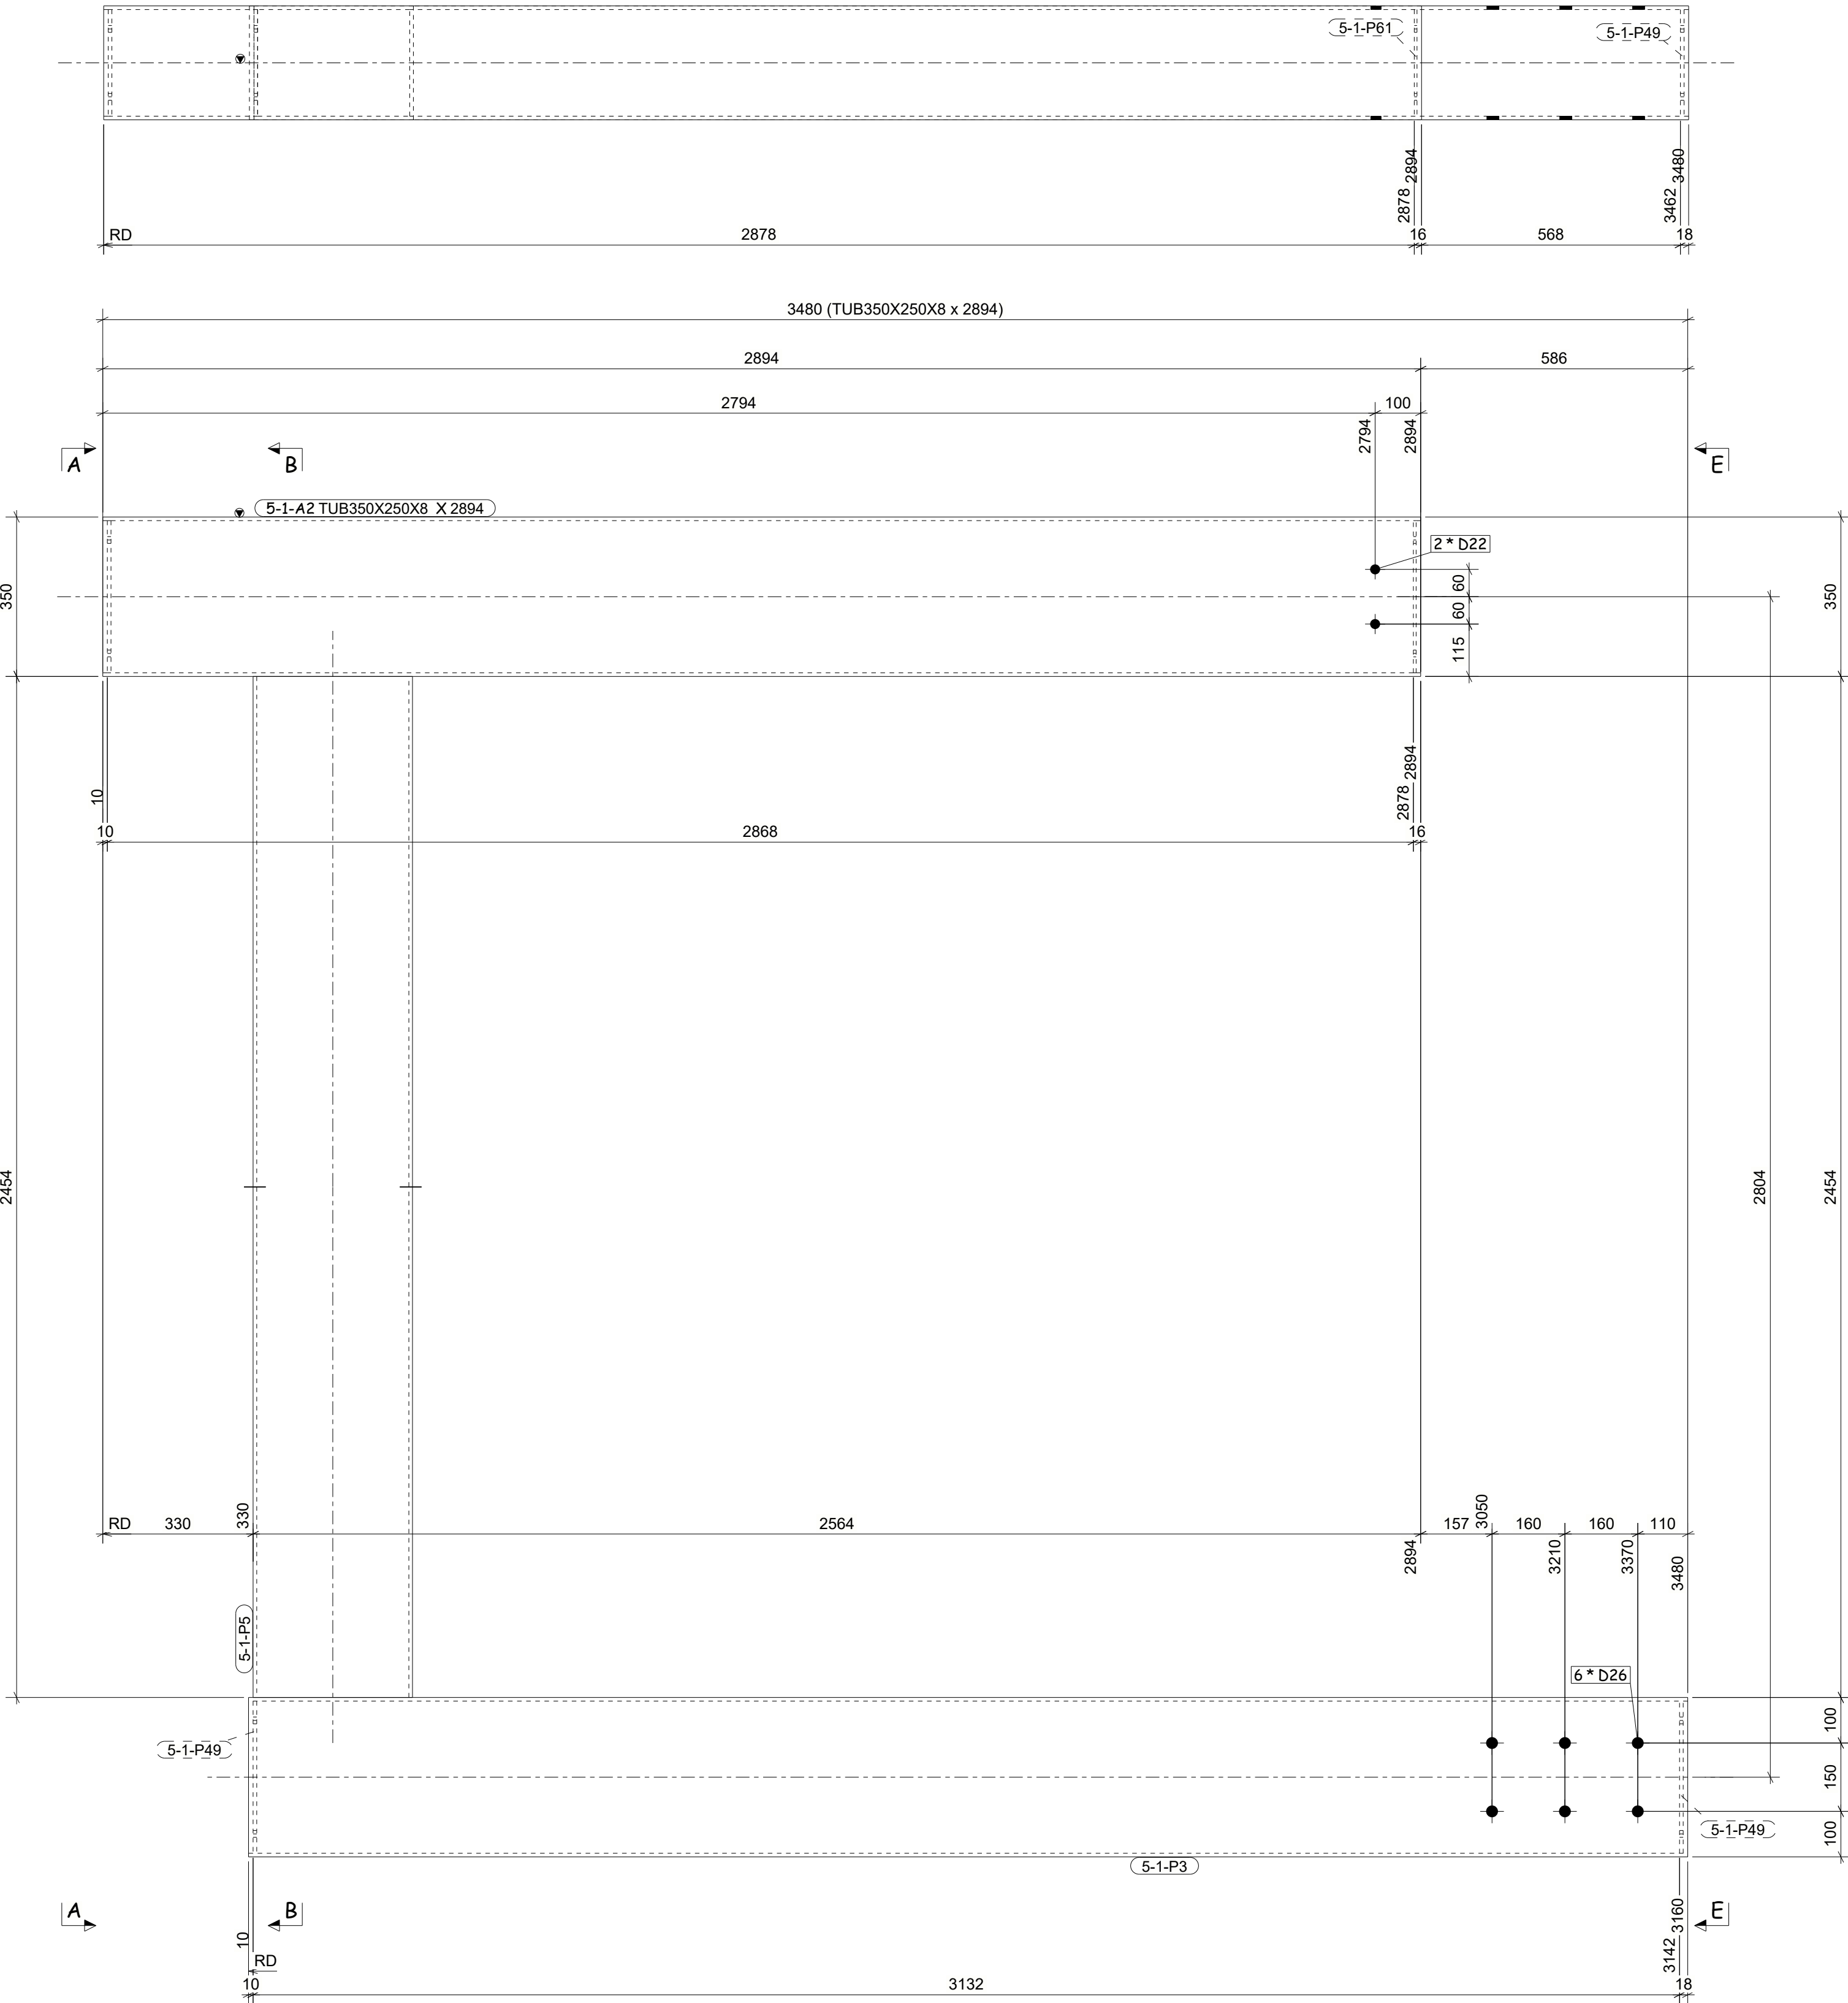

DRAWING NO.: 1μÚŋpÁú-5-1-A2										REV.:													
ERECTION MARK: 1μÚŋpÁú-5-1-A2										DESCRIPTION: FRAME										QTY: 1		NOS	
HOLD :		TYPE :		TREAT :		COST CODE :		REMARKS :															
LENGTH: 3480				WIDTH: 250				HEIGHT: 3154				TOTAL SAREA: 10.9 (M2)											
POS NO.	QTY PER ASSLY	SECTION		LENGTH	UNIT WEIGHT (Kg)	QTY	WEIGHT	GRADE	REVISION	PART ID	TREATMENT	ABENID	TOP F.S.C ABENID	PARTIAL S4 ABENID	MULTIPLE S4 ABENID	SWI NO	REMARKS						
5-1-P2	1	TUB350X250X8		2894	212.246	1	212.246	S275		MM													
5-1-P3	1	TUB350X250X8		3160	231.787	1	231.787	S275		WI													
5-1-P5	1	TUB350X250X8		2454	179.993	1	179.993	S275		WI													
5-1-P49	3	PL8*234		334	4.908	3	14.725	S275		WI													
5-1-P61	1	PL6*234		334	3.681	1	3.681	S275		WI													
					UNIT WEIGHT :-		642.43																
					TOTAL WEIGHT :-		642.43																

1 NO. FRAME MKD' 1μÚŋpÁú-5-1-A2

REV	DATE	DESCRIPTION	DRAWN	CHK'D	APPD.
BUIL'D DESC.		Tekla Corporation			
PROJECT					
CUSTOMER					
SITE LOCATION					
JOB NO.		1μÚŋpÁú	CAD FILES:		1μÚŋpÁú-5-1-A2
DRAWING TITLE:		FRAME SHEET 0	DRAWING NO. :		1μÚŋpÁú-5-1-A2