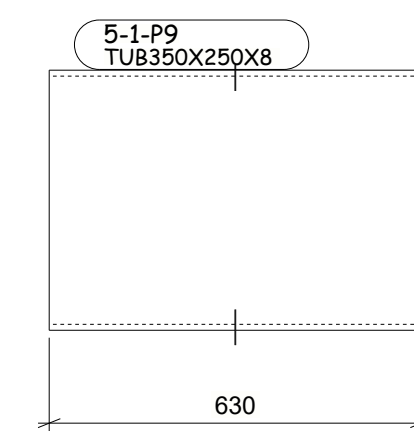
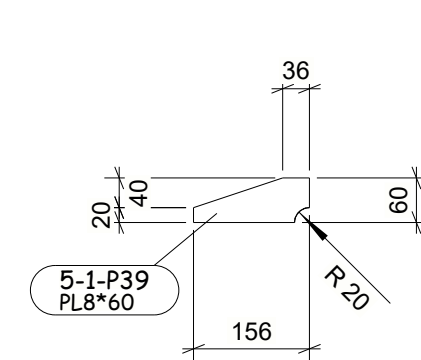
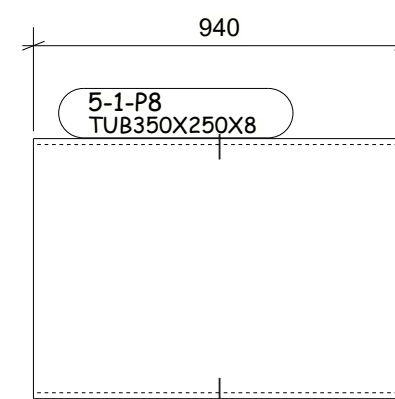
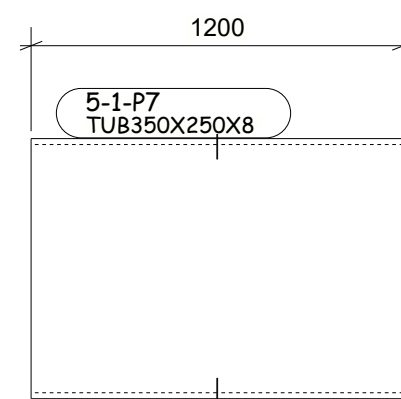
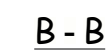
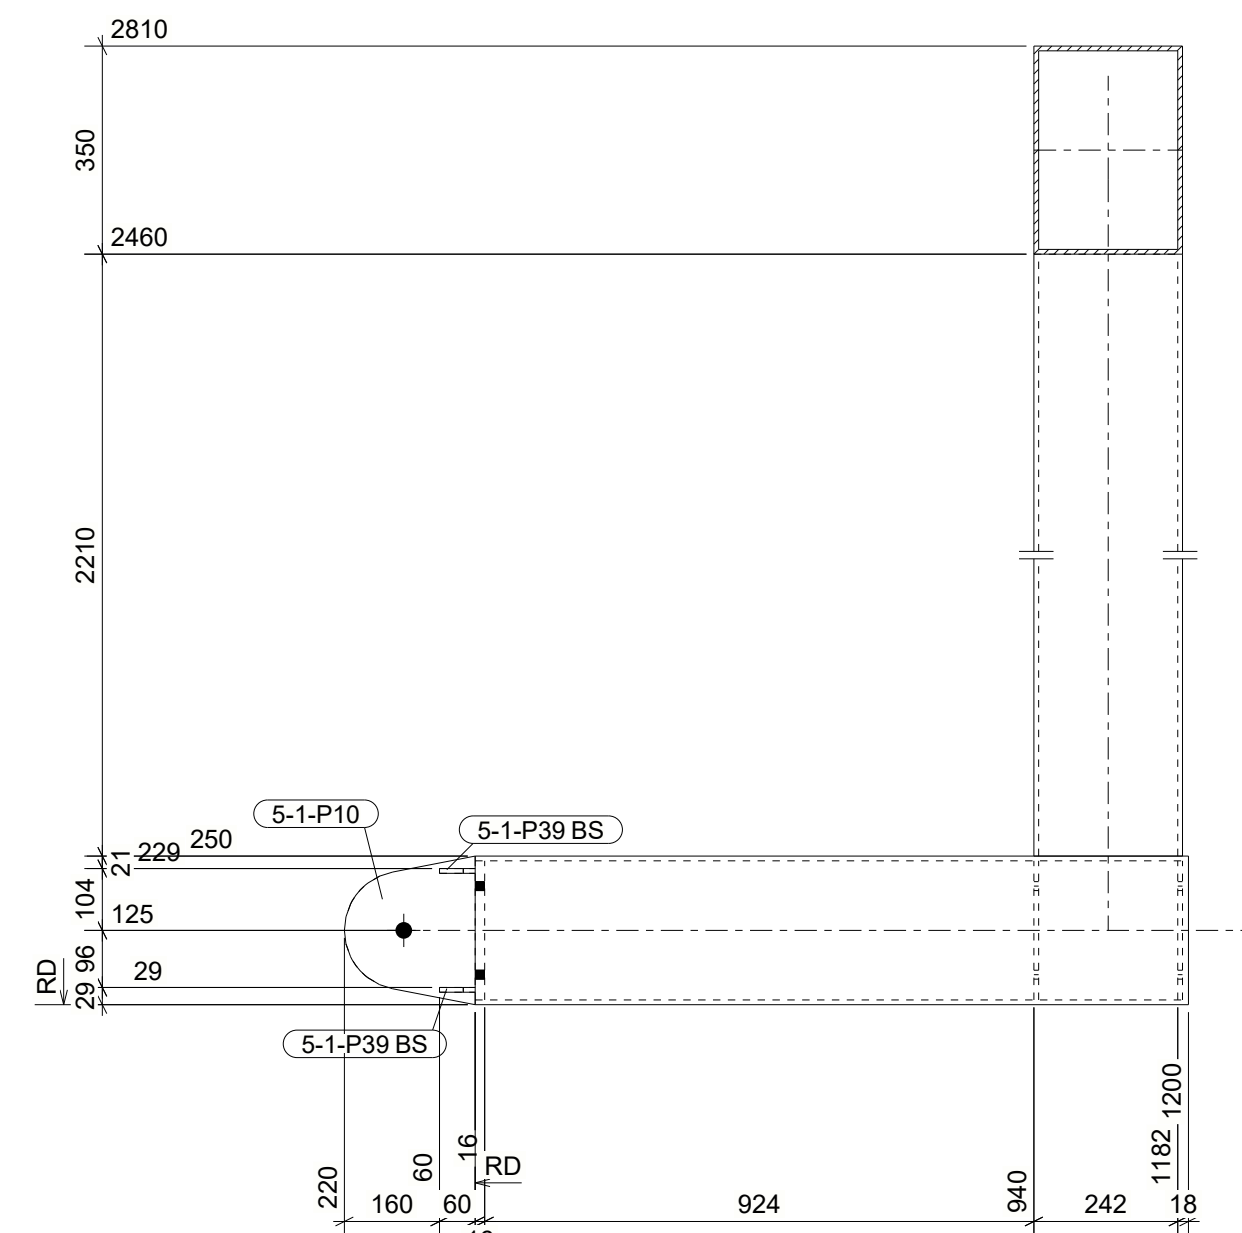
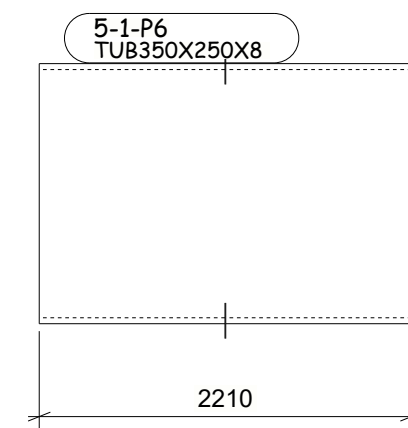
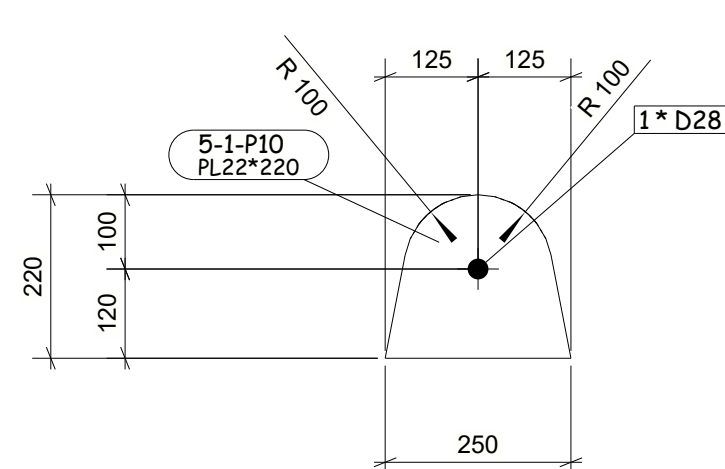
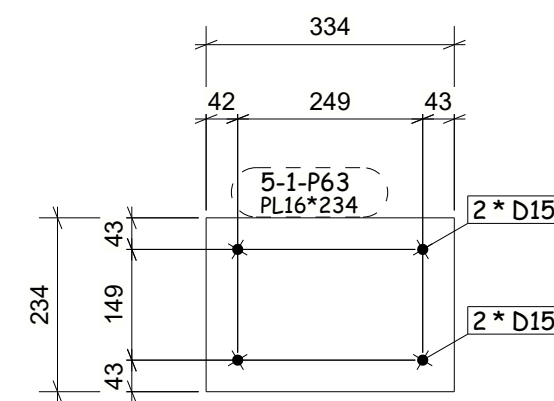
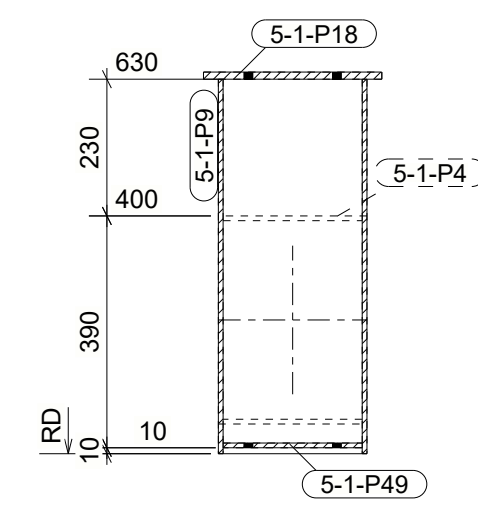
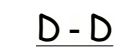
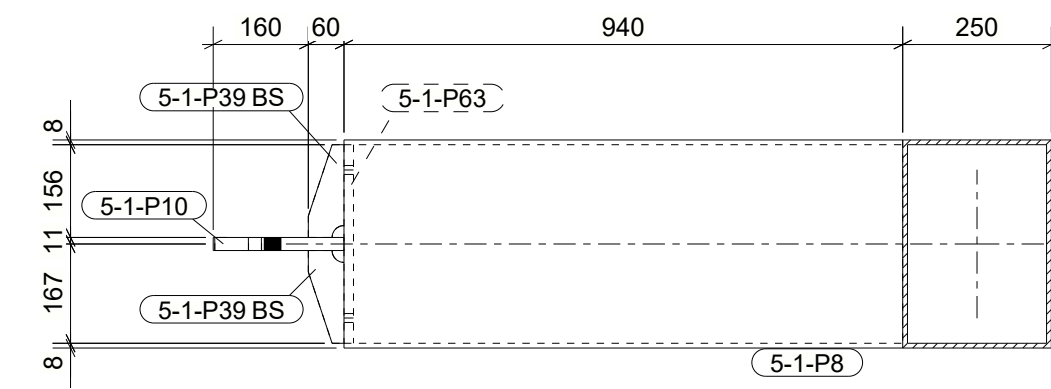
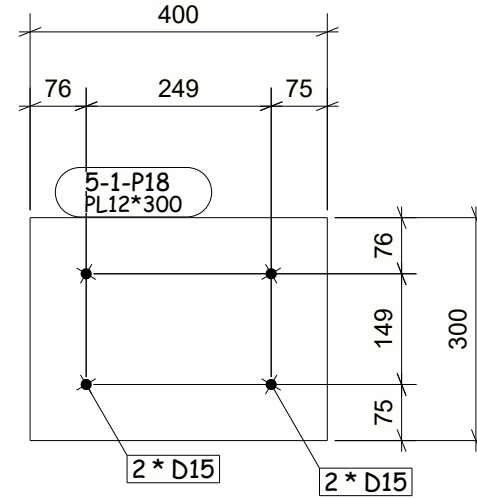
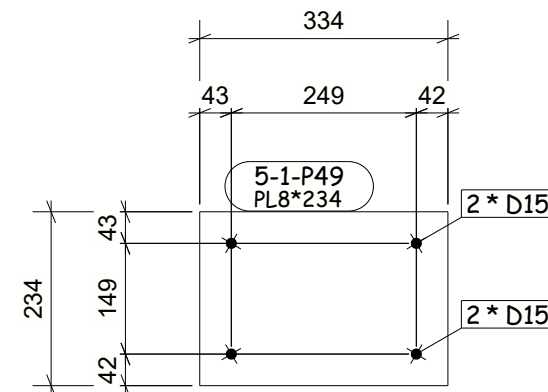
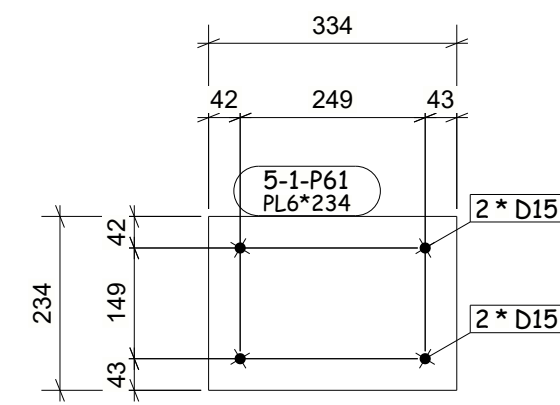
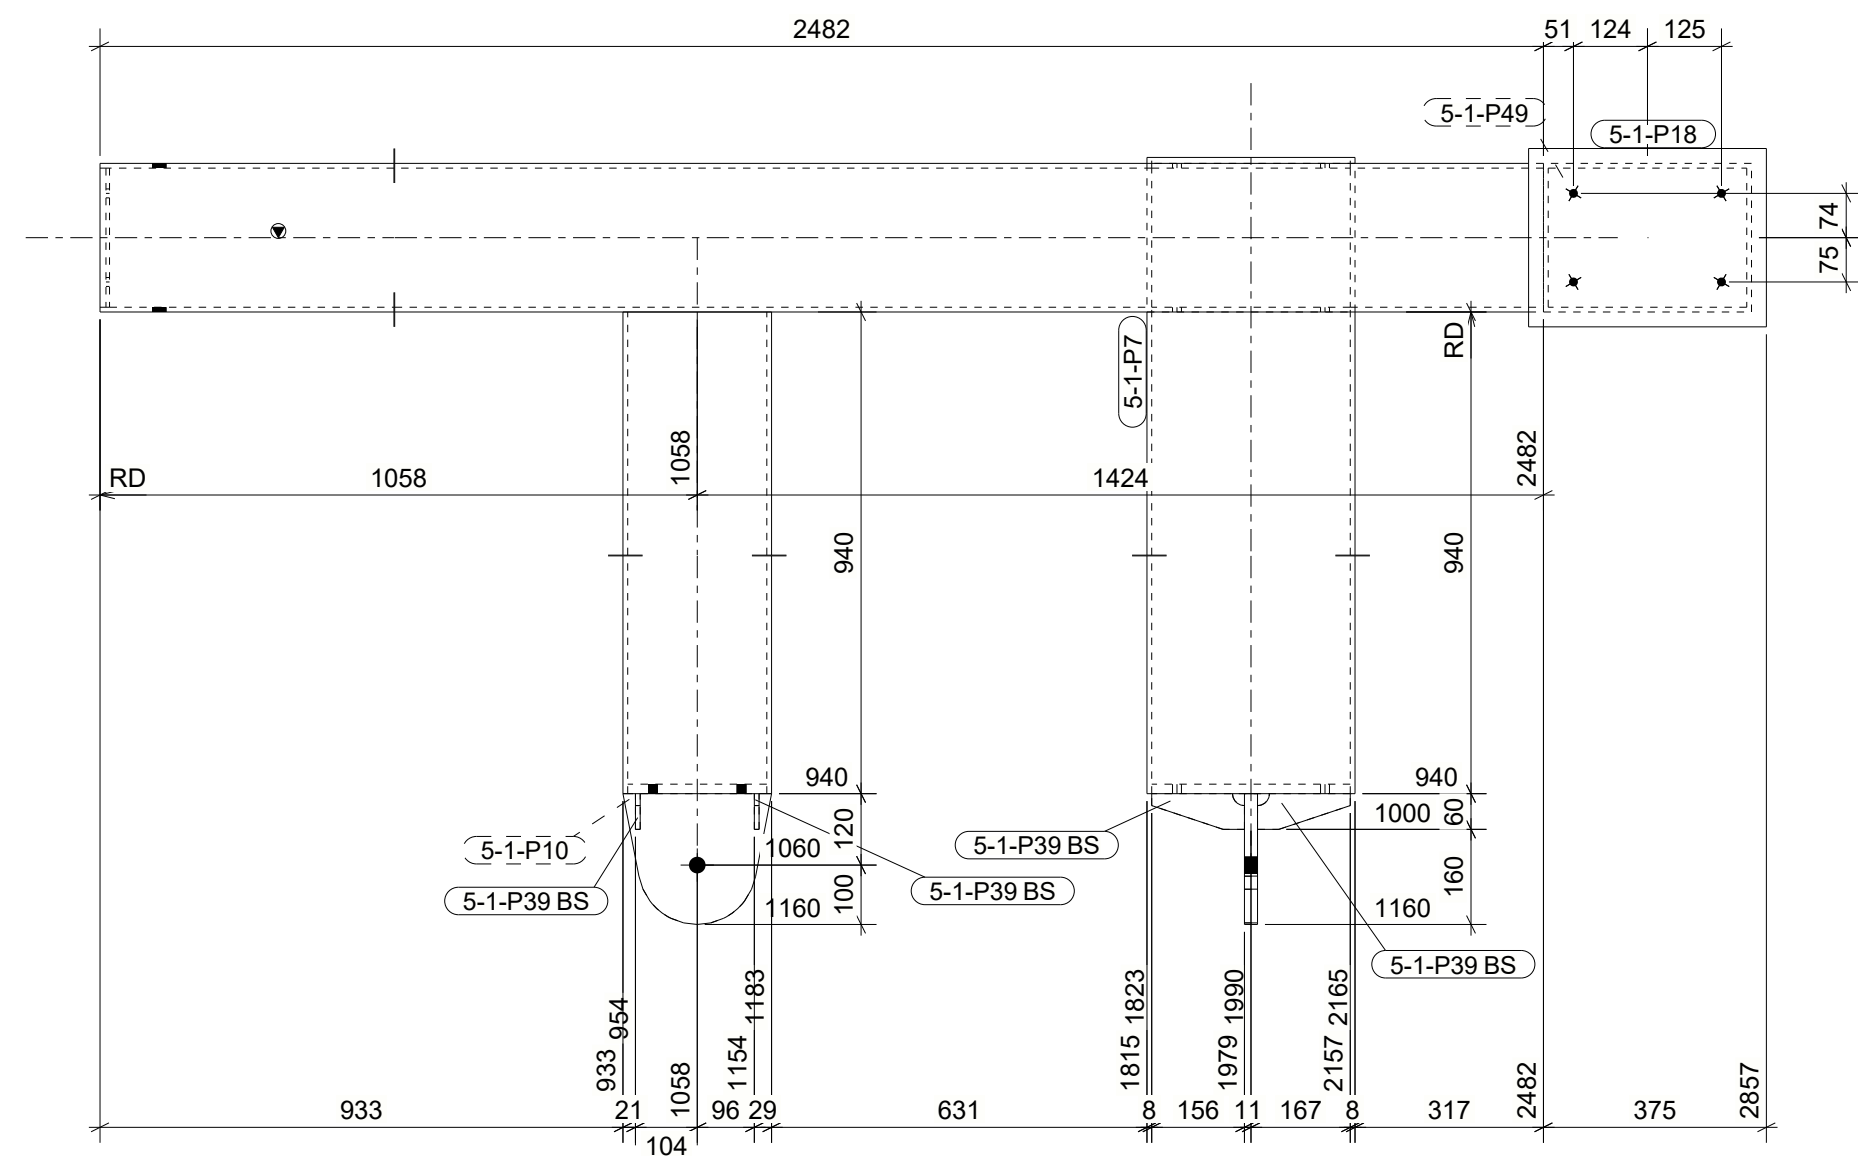


DRAWING NO. : 1PUBA-5-1-A5										REV. :									
ERECTION MARK : 1PUBA-5-1-A5				DESCRIPTION : FRAME				QTY : 1		NOS									
HOLD :		TYPE :		TREAT :		COST CODE :		REMARKS :											
LENGTH : 2857		WIDTH : 1435		HEIGHT : 3052		TOTAL S.AREA : 10.5		(M2)											
POS NO.	QTY PER ASSLY	SECTION	LENGTH	UNIT WEIGHT (Kg)	TOTAL		GRADE	REVISION	PART ID	TREATMENT	ABRN ID	TOP FSC	INTERNAL SA	ABRN SA	MULTI FSC	ABRN FSC	SW NO	REMARKS	
					QTY	WEIGHT													
5-1-P4	1	TUB350X250X8	2482	182.032	1	182.032	S275			MM									
5-1-P6	1	TUB350X250X8	2210	162.129	1	162.129	S275			WI									
5-1-P7	1	TUB350X250X8	1200	88.013	1	88.013	S275			WI									
5-1-P8	1	TUB350X250X8	940	68.942	1	68.942	S275			WI									
5-1-P9	1	TUB350X250X8	630	46.211	1	46.211	S275			WI									
5-1-P10	2	PL22*220	250	9.498	2	18.997	S275			WI									
5-1-P18	1	PL12*300	400	11.304	1	11.304	S275			WI									
5-1-P39	8	PL8*60	156	0.588	8	4.702	S275			WI									
5-1-P49	3	PL8*234	334	4.908	3	14.725	S275			WI									
5-1-P61	1	PL6*234	334	3.681	1	3.681	S275			WI									
5-1-P63	2	PL16*234	334	9.816	2	19.633	S275			WI									
				UNIT WEIGHT :-		620.37													
				TOTAL WEIGHT :-		620.37													

REV	DATE	DESCRIPTION	DRAWN	CHK'D	APPD.
BUIL'D DESC.	Tekla Corporation				
PROJECT					
CUSTOMER					
SITE LOCATION					
JOB NO.	1μ011bAú		CAD FILES:		
			1μ011bAú-5-1-A5		
DRAWING TITLE:	FRAME SHEET 0		DRAWING NO. :		
			1μ011bAú-5-1-A5		