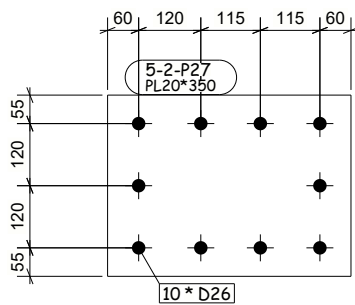
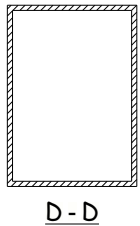
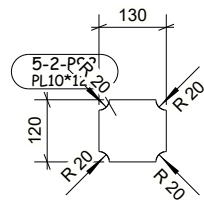
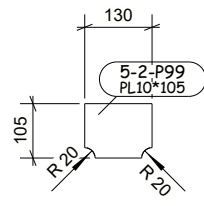
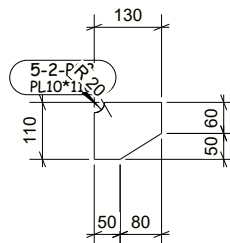
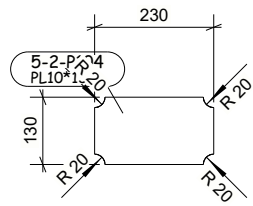
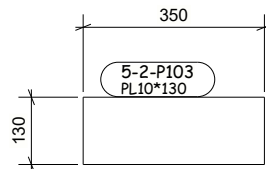
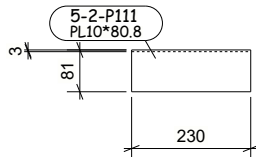
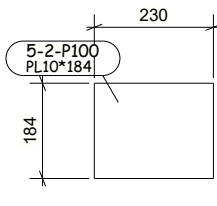
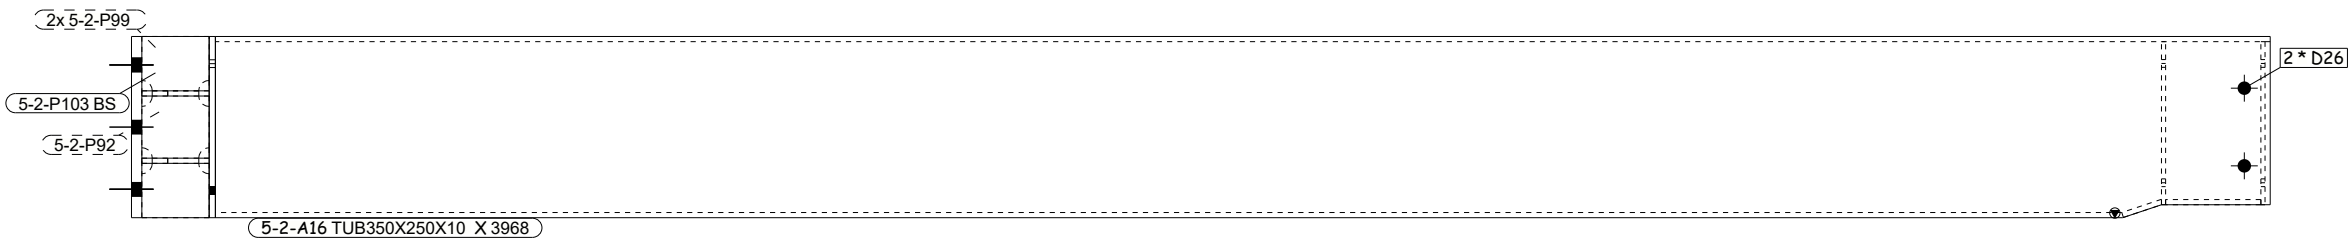
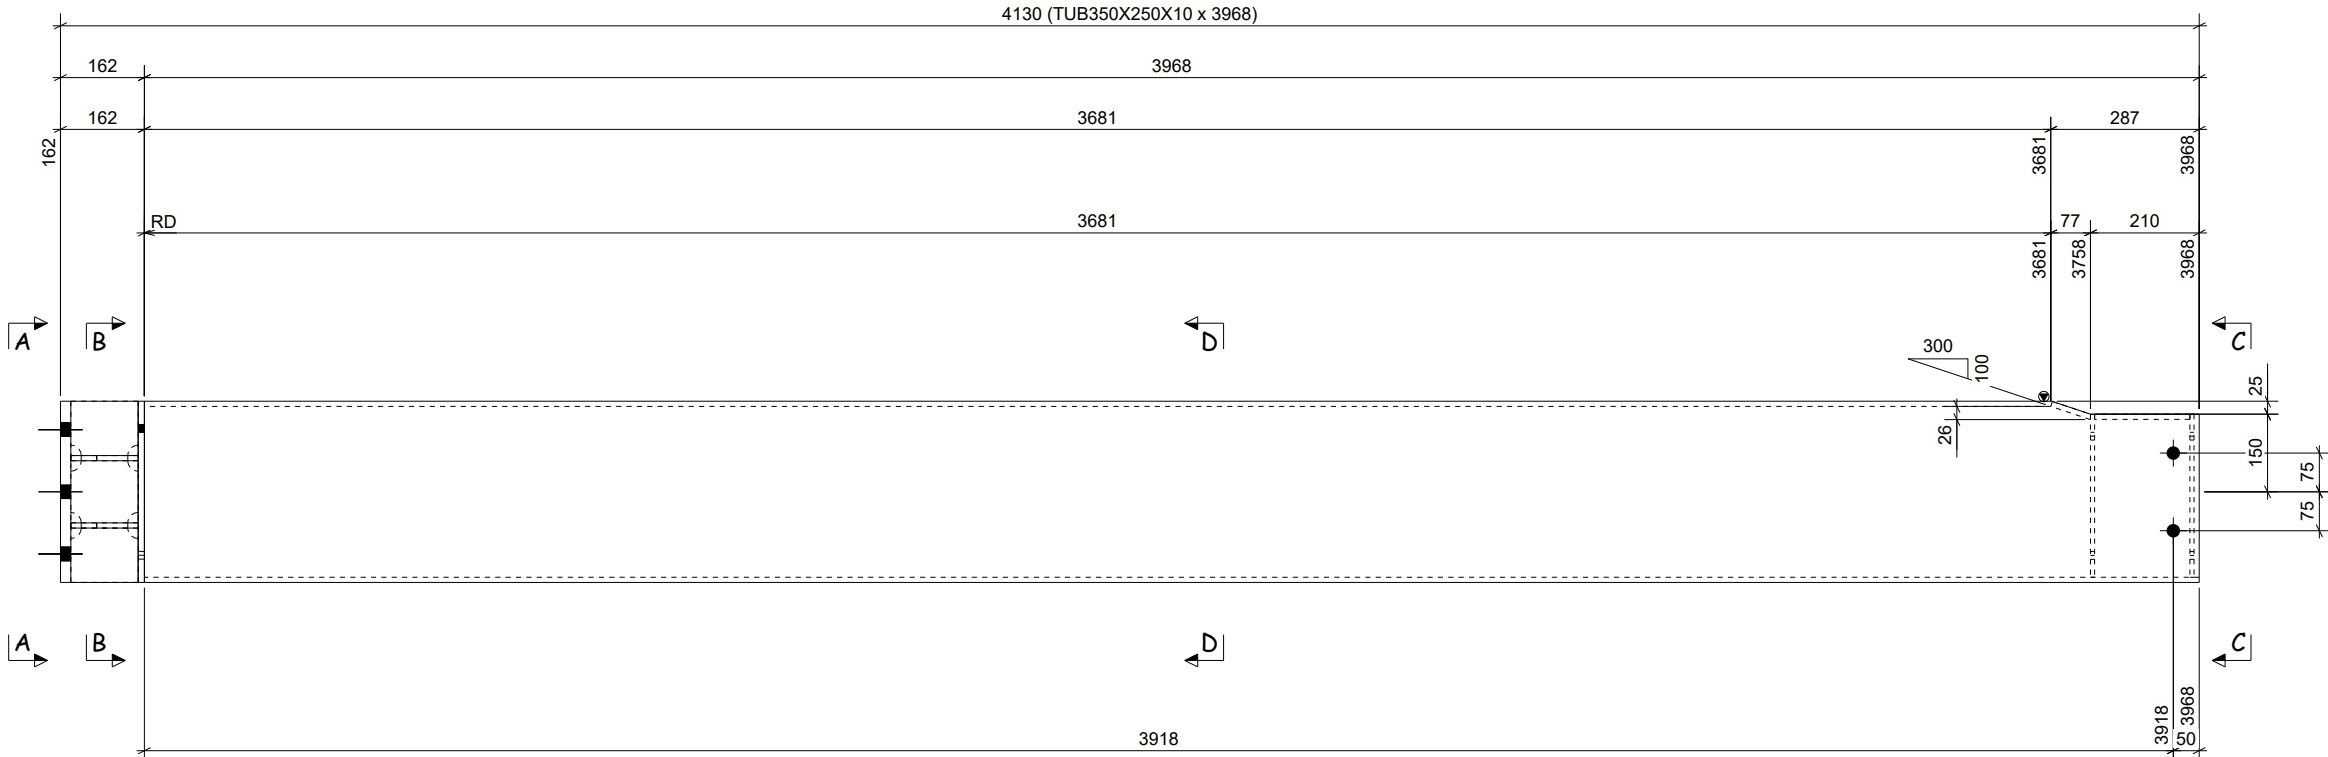
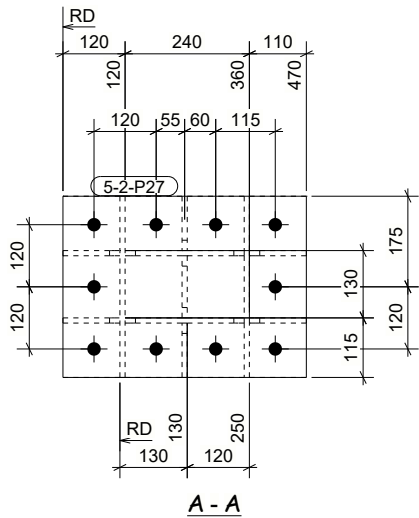
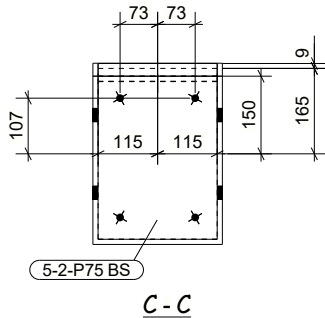
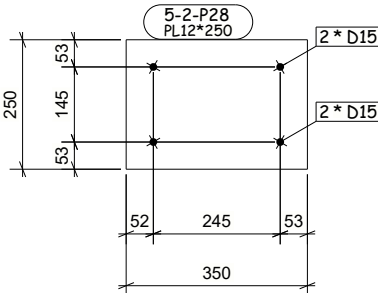
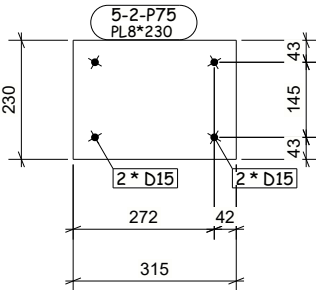
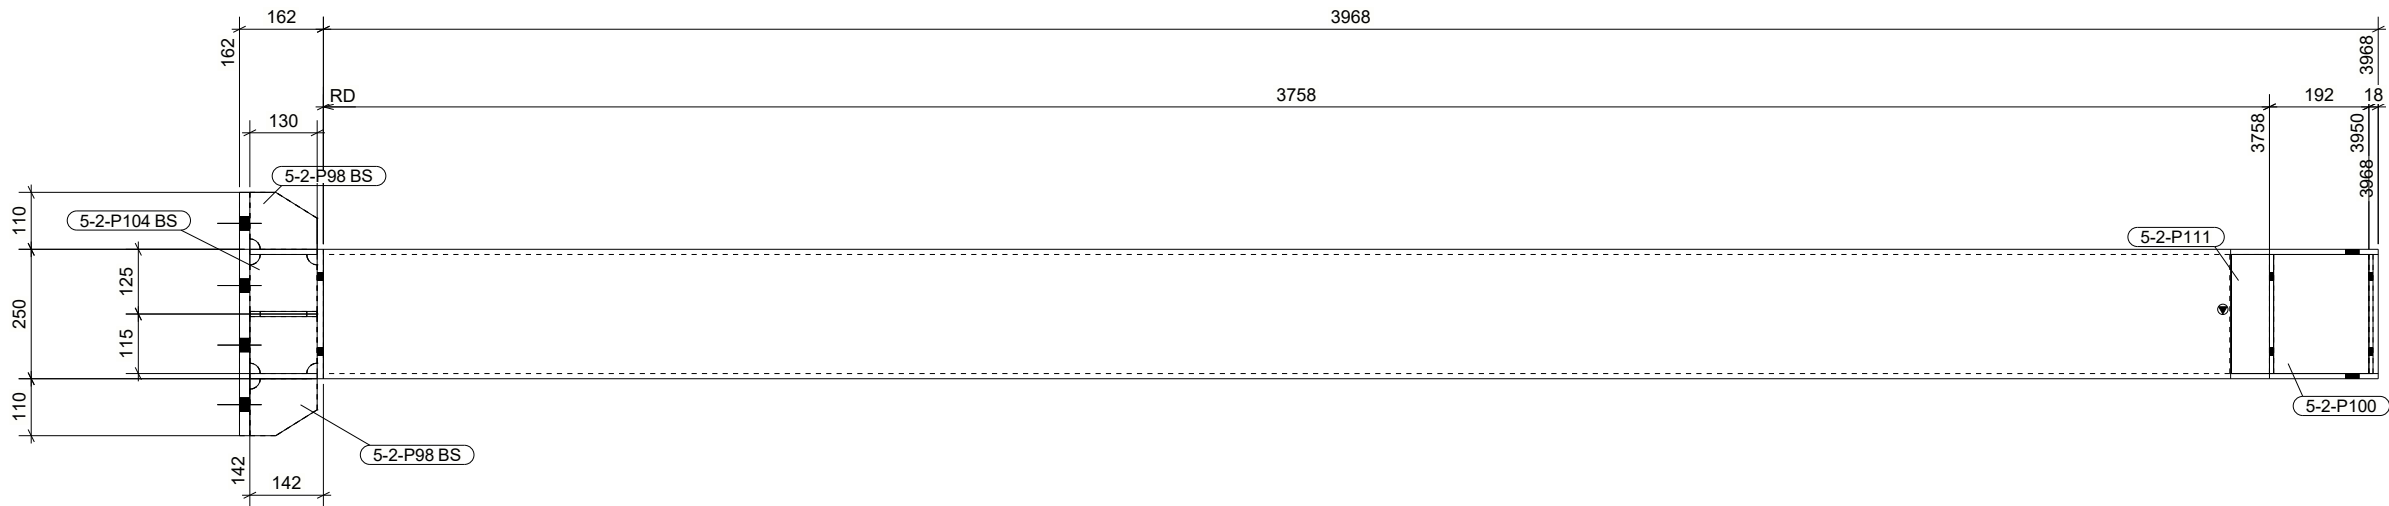


DRAWING NO. : 1μÚŋpÁú-5-2-A16										REV.:									
ERECTION MARK : 1μÚŋpÁú-5-2-A16										DESCRIPTION : BEAM									
HOLD : TYPE : TREAT : COST CODE : REMARKS :										QTY : 1 NOS									
LENGTH : 4130 WIDTH : 470 HEIGHT : 350										TOTAL S.AREA : 6.2 (M2)									
POS NO.	QTY PER ASSLY	SECTION	LENGTH	UNIT WEIGHT (Kg)	TOTAL		GRADE	REVISION	PART ID	TREATMENT	ABBV ID	TOP F.S.C	ABBV ID	PARTIAL S.A	ABBV ID	MULTIPLE S.C	ABBV ID	SW/NO	REMARKS
5-2-P87	1	TUB350X250X10	3968	361.326	1	361.326	S275		MM										
5-2-P27	1	PL20*350	470	25.826	1	25.826	S275		WI										
5-2-P28	1	PL12*250	350	8.243	1	8.243	S275		WI										
5-2-P75	2	PL8*230	315	4.549	2	9.099	S275		WI										
5-2-P92	1	PL10*120	130	1.225	1	1.225	S275		WI										
5-2-P98	4	PL10*110	130	1.123	4	4.490	S275		WI										
5-2-P99	2	PL10*105	130	1.072	2	2.143	S275		WI										
5-2-P100	1	PL10*184	230	3.322	1	3.322	S275		WI										
5-2-P103	2	PL10*130	350	3.572	2	7.144	S275		WI										
5-2-P104	2	PL10*130	230	2.347	2	4.694	S275		WI										
5-2-P111	1	PL10*80.8	230	1.459	1	1.459	S275		WI										
				UNIT WEIGHT :-		428.97													
				TOTAL WEIGHT :-		428.97													

1 NO. BEAM MKD' 1μÚŋpÁú-5-2-A16

REV	DATE	DESCRIPTION	DRAWN	CHK'D	APPD.
BUIL'D DESC.		Tekla Corporation			
PROJECT					
CUSTOMER					
SITE LOCATION					
JOB NO.		1μÚŋpÁú	CAD FILES:		
DRAWING TITLE:		BEAM SHEET 0	DRAWING NO. : 1μÚŋpÁú-5-2-A16		