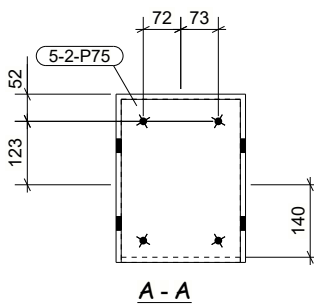
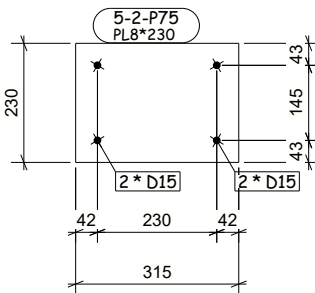
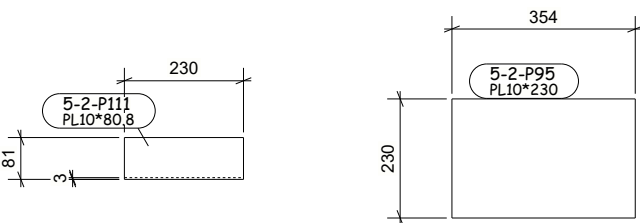
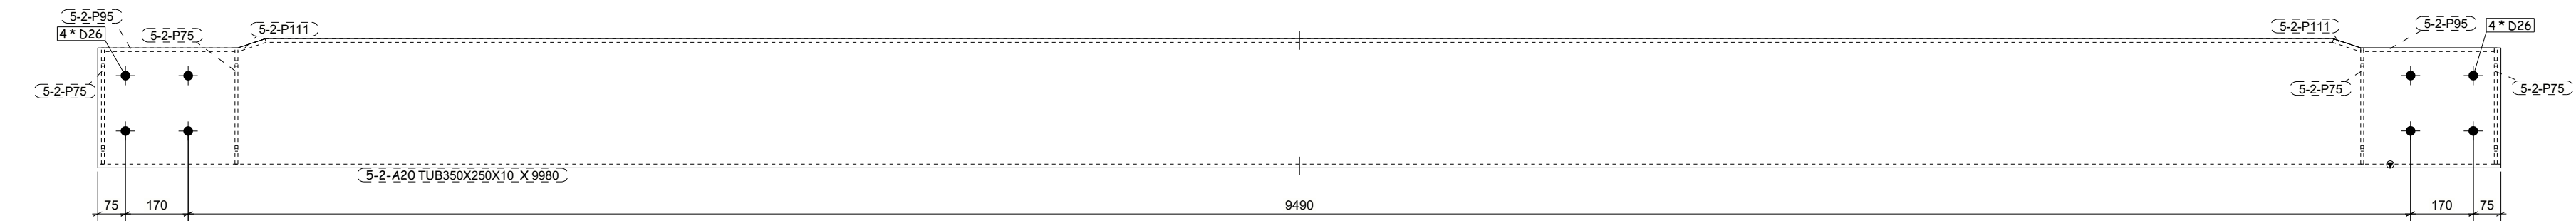
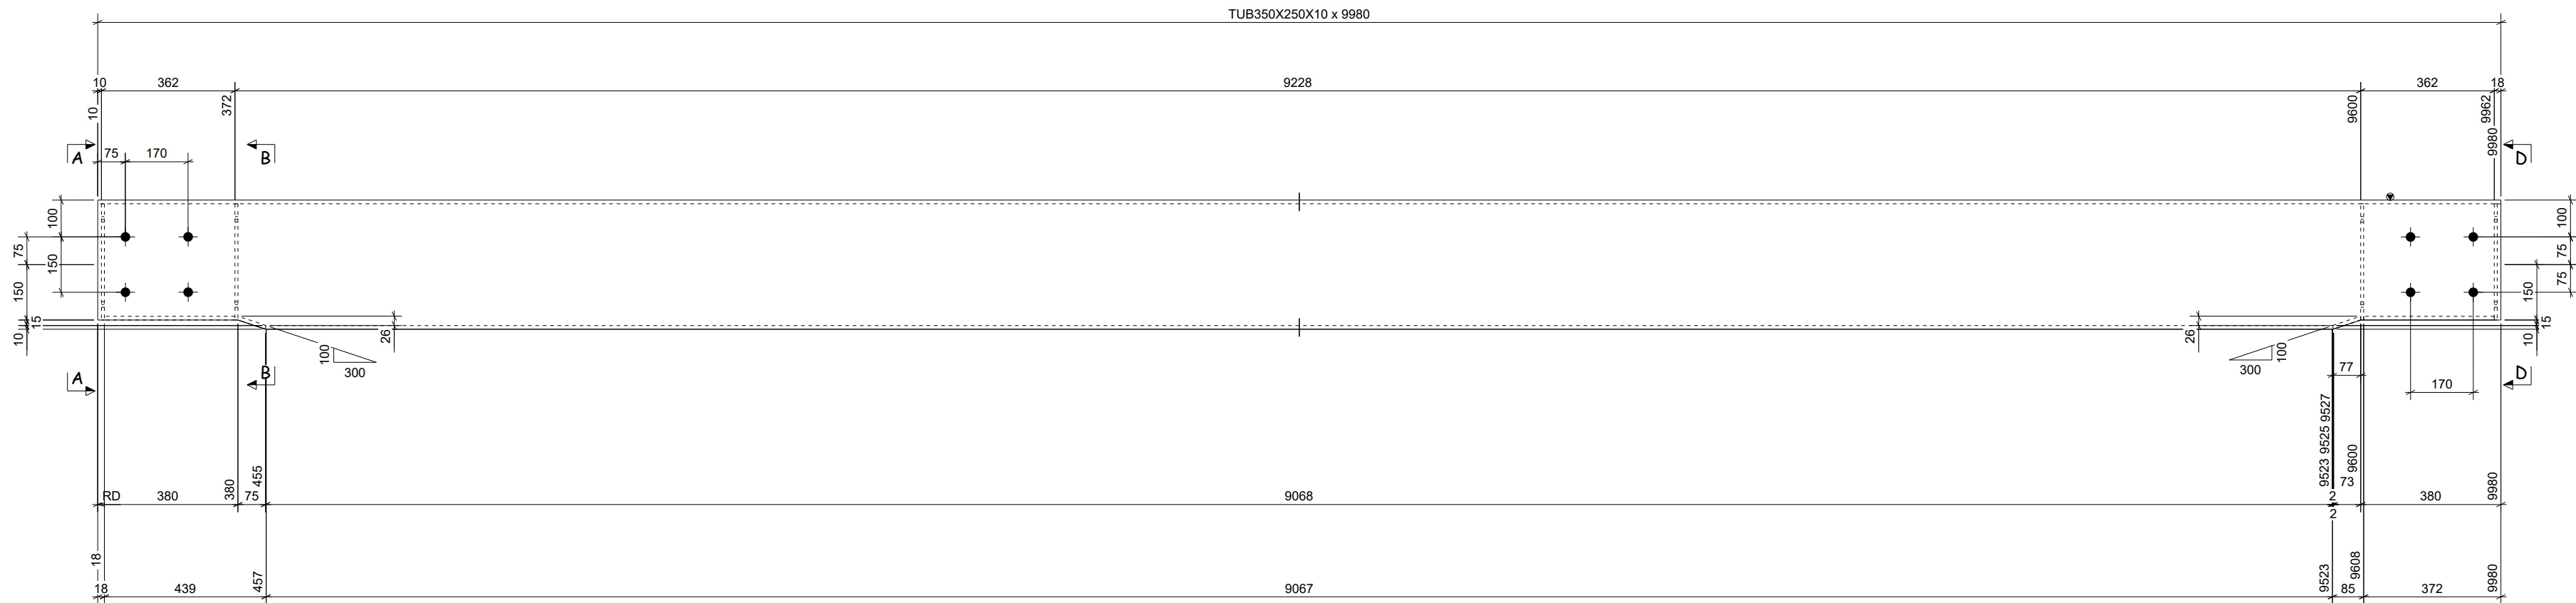
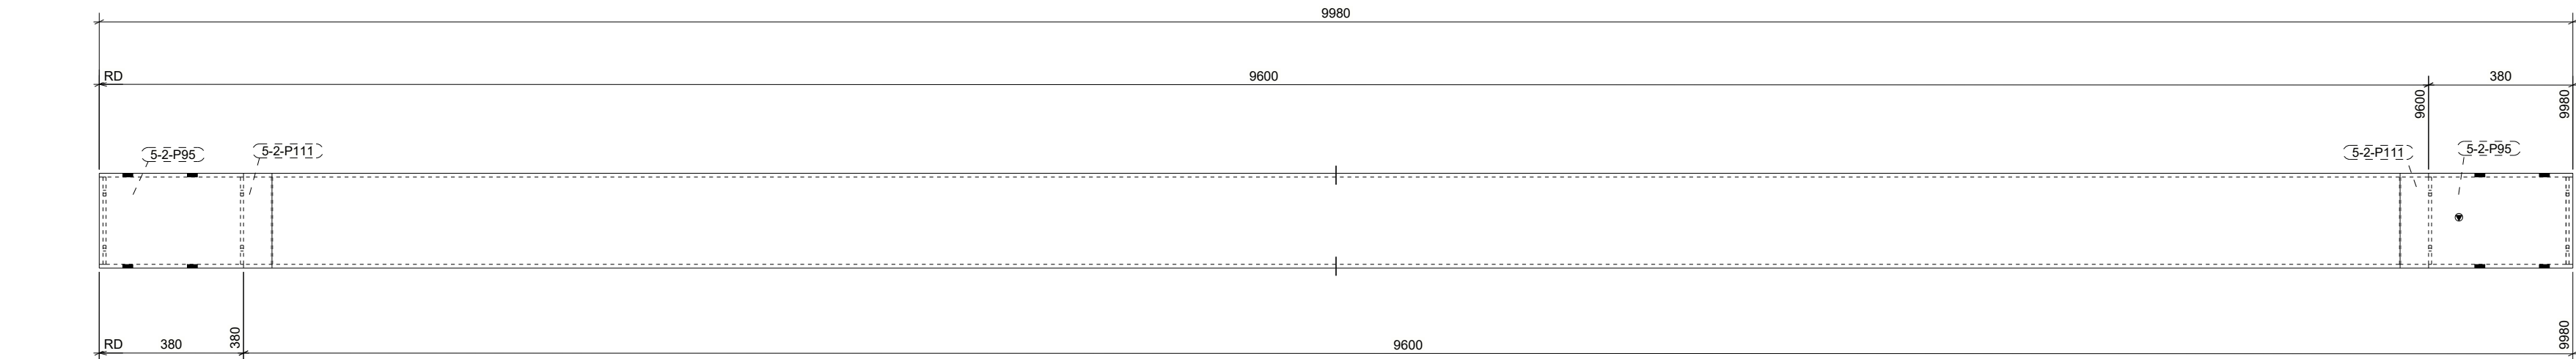


DRAWING NO. : 1μÚŋpÁú-5-2-A20										REV.:									
ERECTION MARK : 1μÚŋpÁú-5-2-A20										DESCRIPTION : BEAM									
HOLD : TYPE : TREAT : COST CODE : REMARKS :										QTY: 1 NOS									
LENGTH : 9980										WIDTH : 250									
HEIGHT : 350										TOTAL SAREA : 12.7 (M2)									
POS NO.	QTY PER ASSLY	SECTION		LENGTH	UNIT WEIGHT (Kg)	TOTAL QTY	WEIGHT	GRADE	REVISION	PART ID	TREATMENT	ABRN ID	TOP F.S.C. ABRN ID	PARTIAL S.A ABRN ID	MULTIPLY F.S.C. ABRN ID	SWI NO	REMARKS		
5-2-P30	1	TUB350X250X10		9980	908.779	1	908.779	S275		MM									
5-2-P75	4	PL8*230		315	4.550	4	18.199	S275		WI									
5-2-P95	2	PL10*230		354	6.391	2	12.783	S275		WI									
5-2-P111	2	PL10*80.8		230	1.459	2	2.917	S275		WI									
					UNIT WEIGHT :-		942.68												
					TOTAL WEIGHT :-		942.68												

1 NO. BEAM MKD' 1μÚŋpÁú-5-2-A20

REV	DATE	DESCRIPTION	DRAWN	CHK'D	APPD.
BUIL'D DESC.		Tekla Corporation			
PROJECT					
CUSTOMER					
SITE LOCATION					
JOB NO.		1μÚŋpÁú	CAD FILES:		
DRAWING TITLE:		BEAM SHEET 0		DRAWING NO. :	
				1μÚŋpÁú-5-2-A20	