
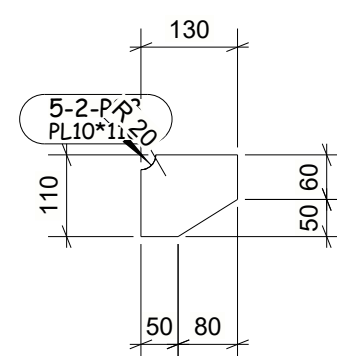
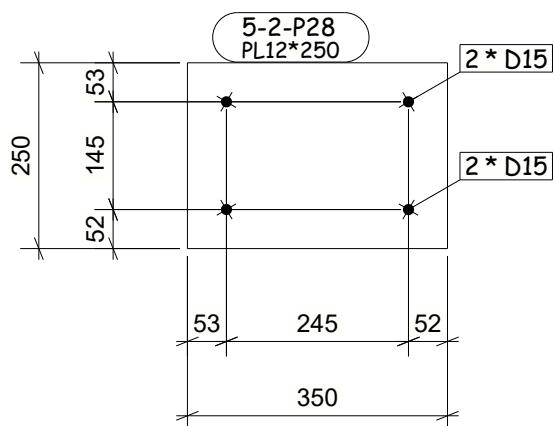
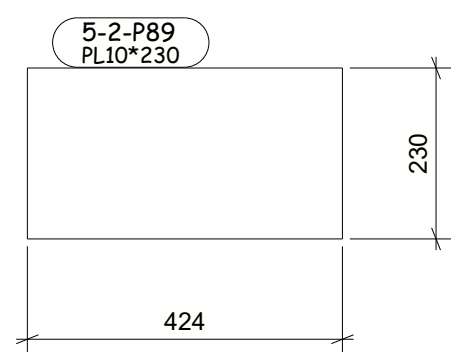
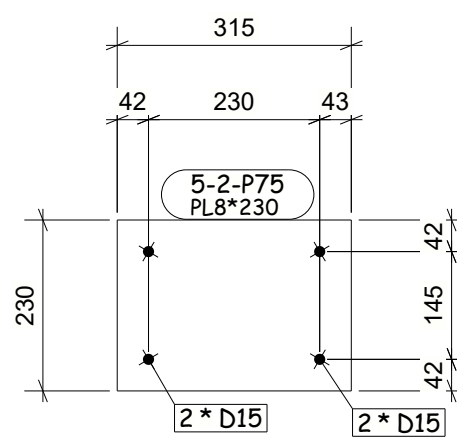
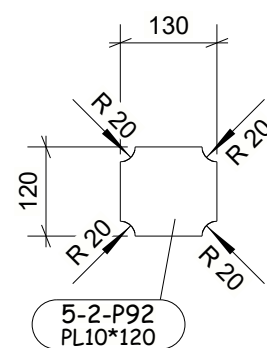
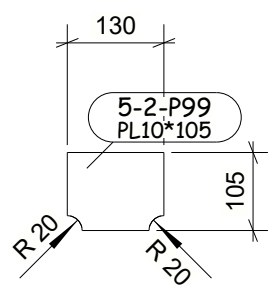
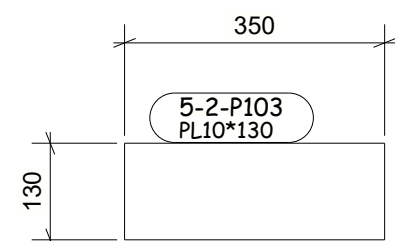
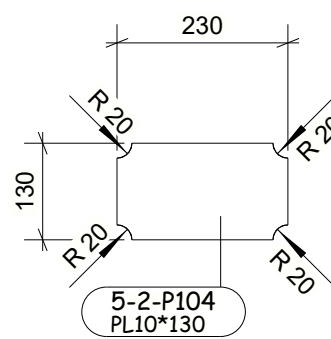
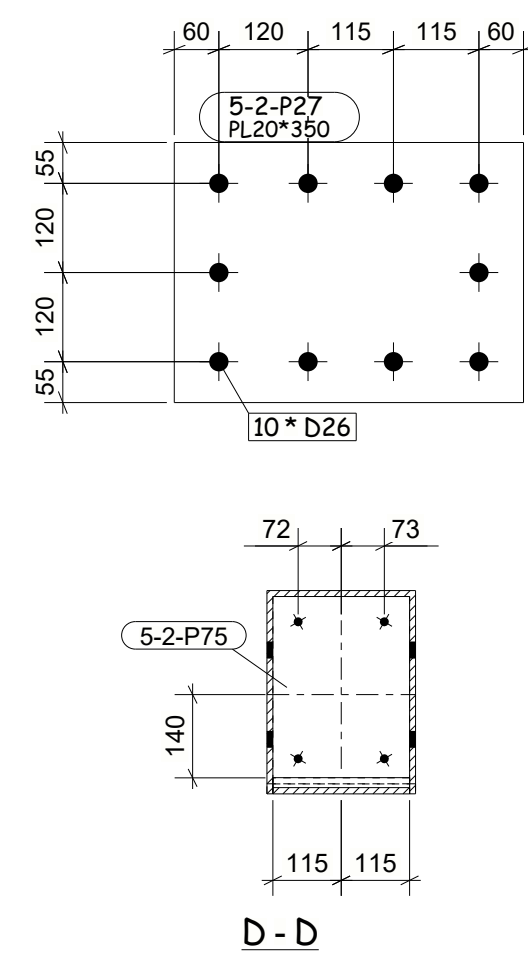
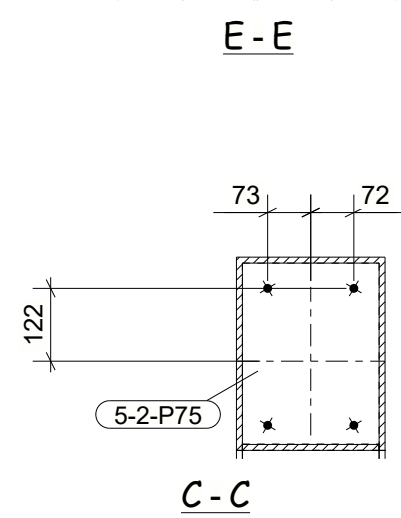
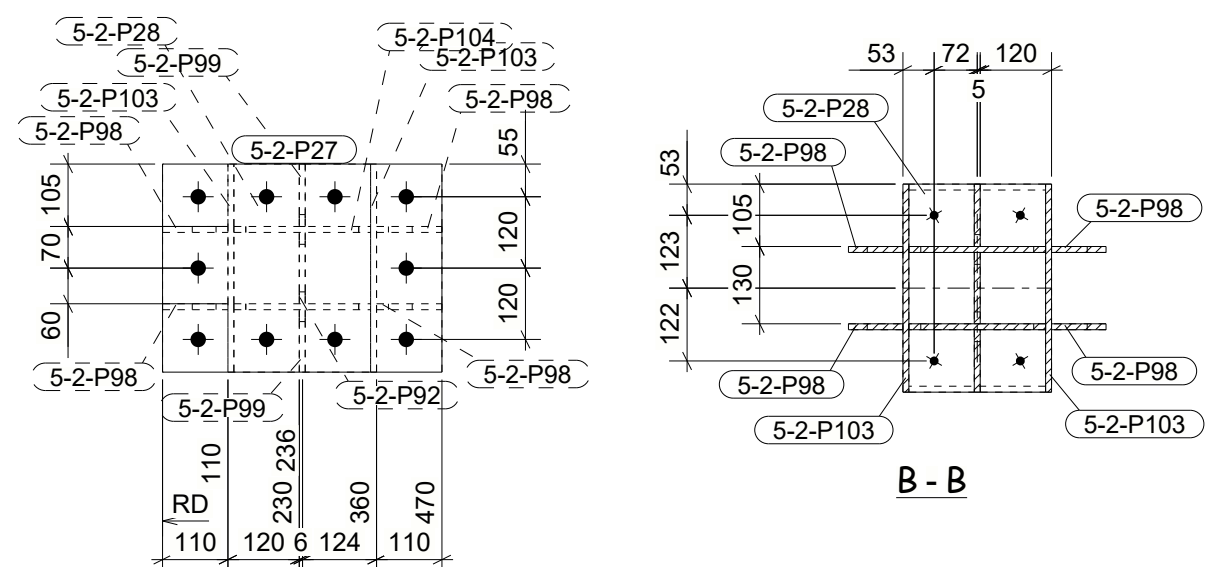
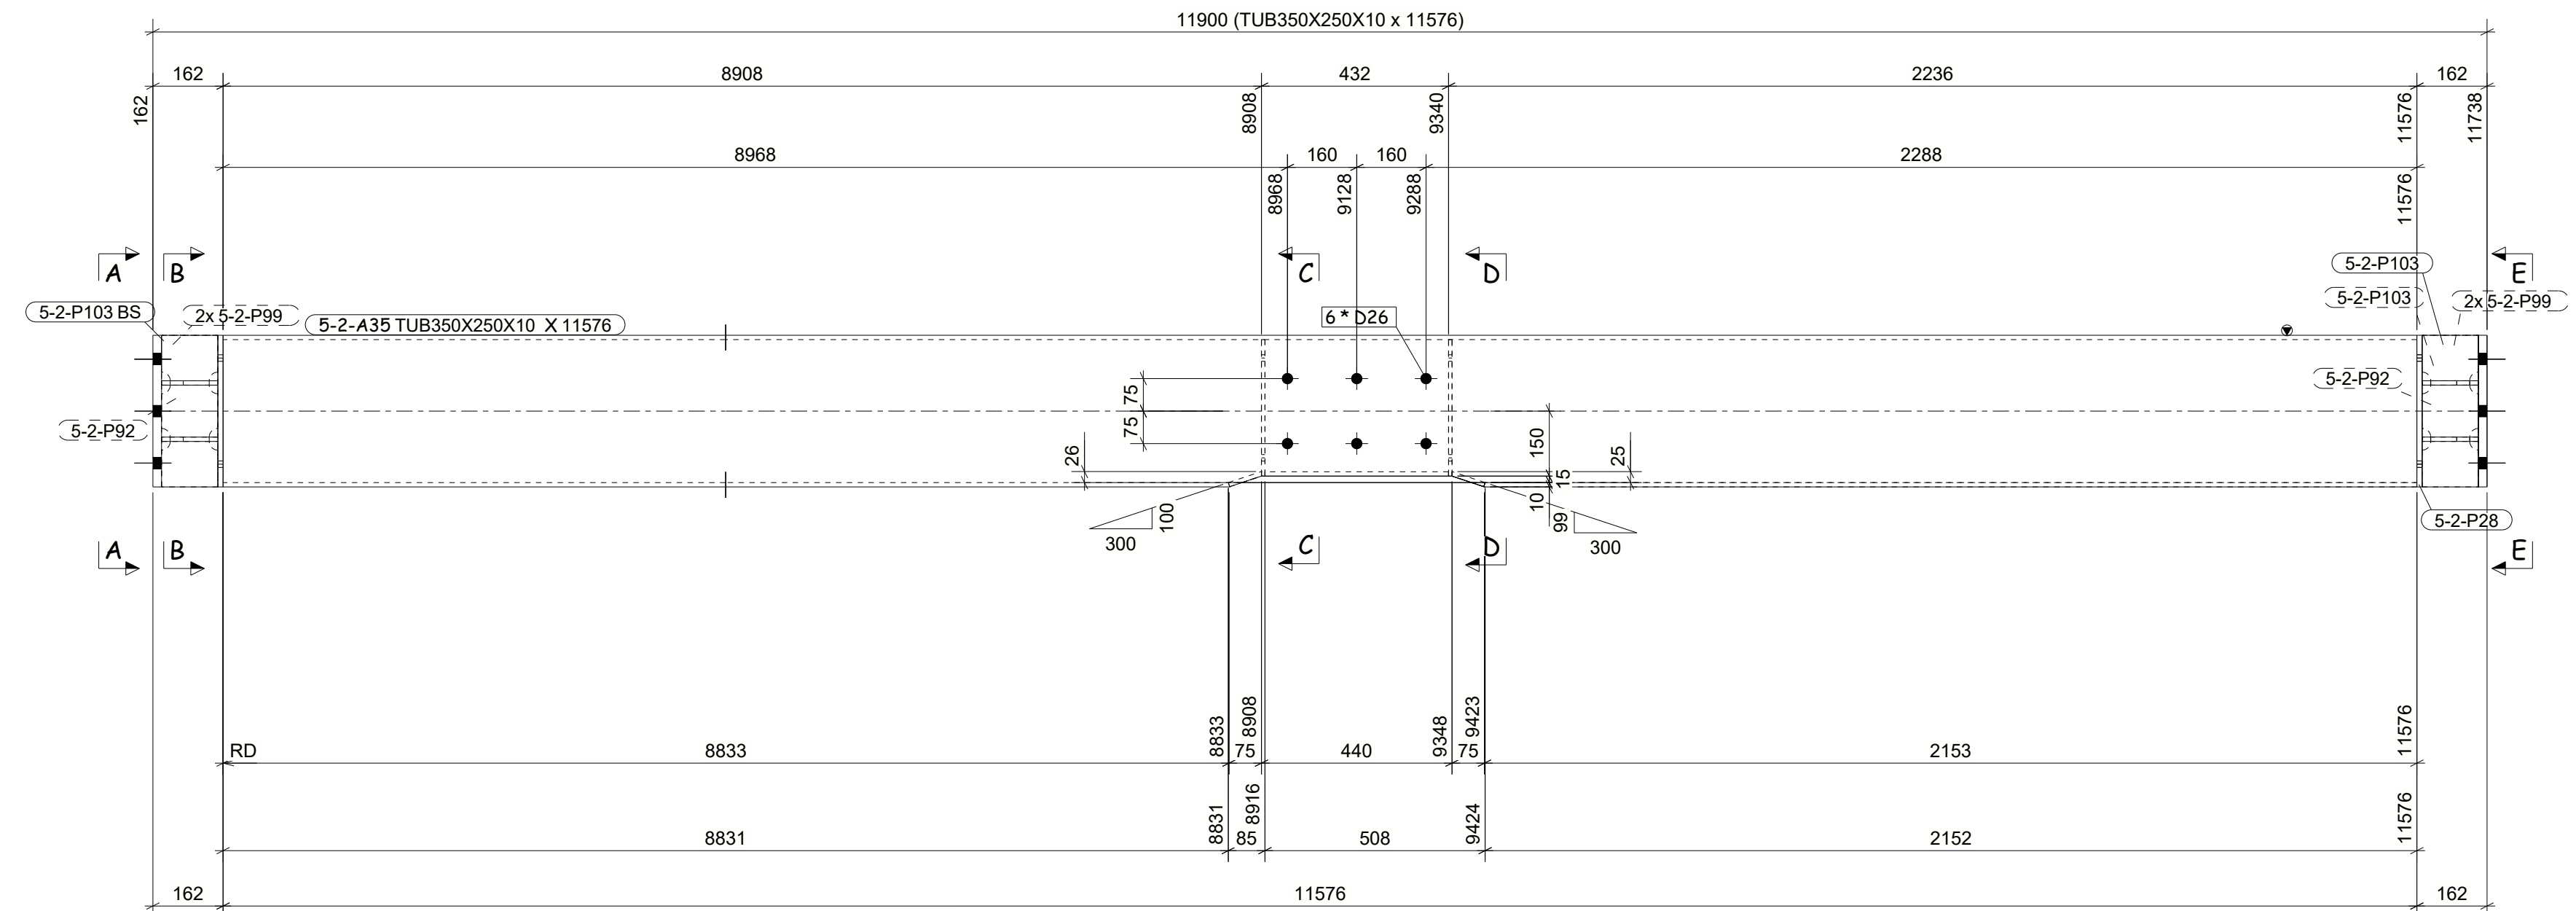
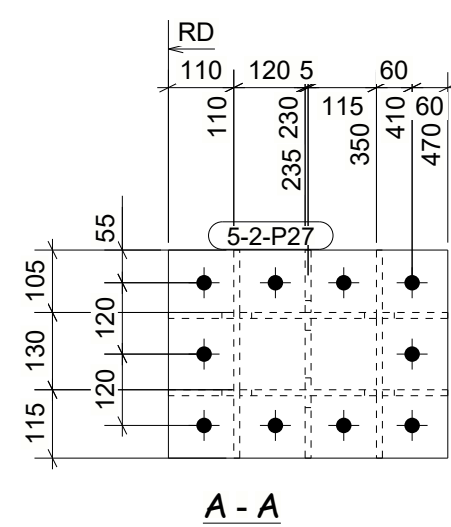
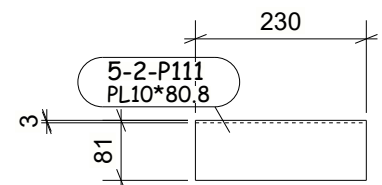


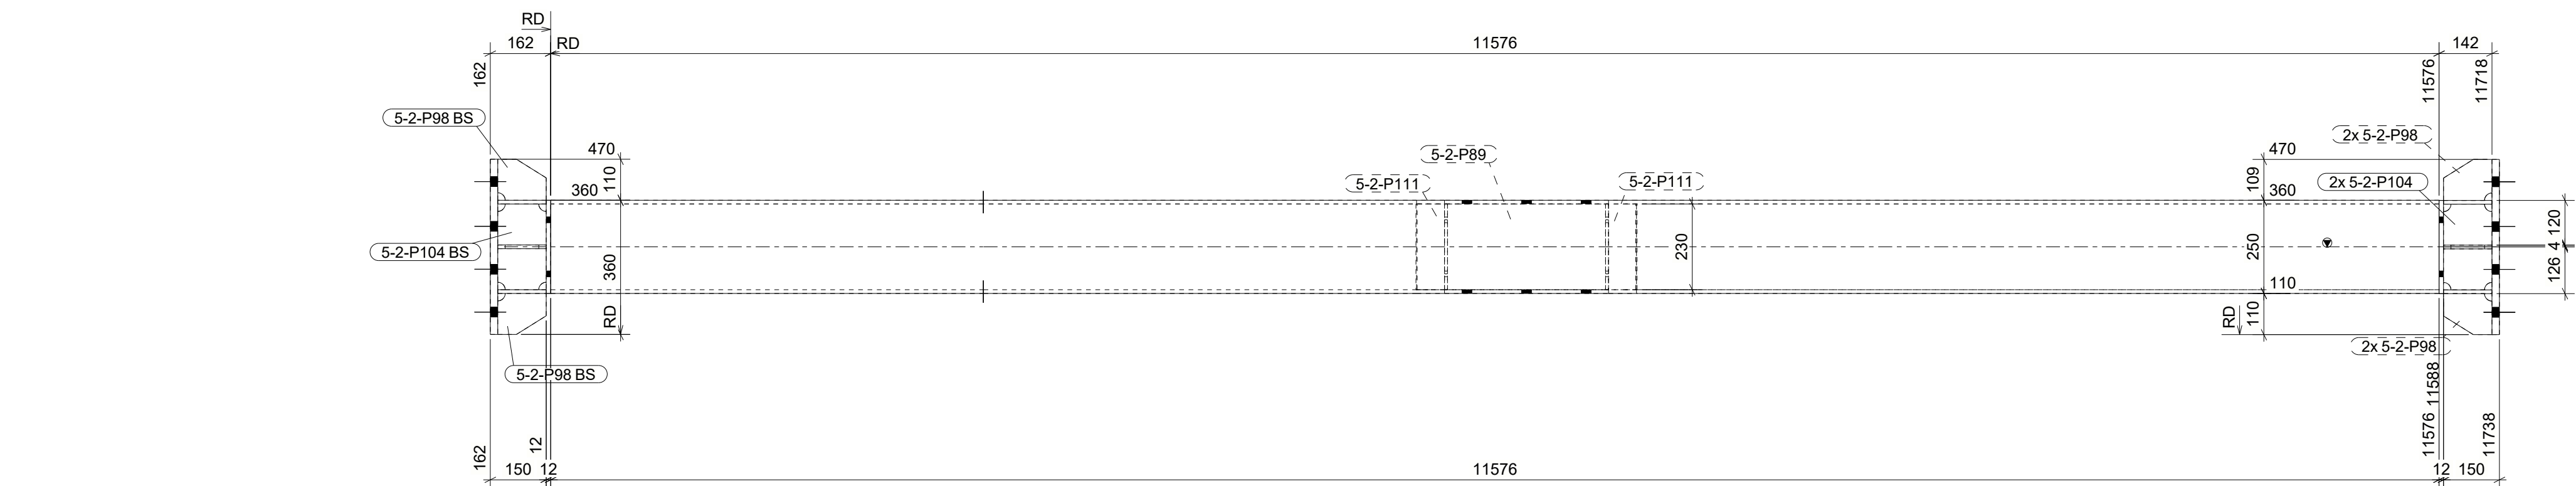

DRAWING NO. : 1μΠΑΔ-5-2-A35

REV. :

ERECTION MARK : 1μΠΑΔ-5-2-A35

DESCRIPTION : FRAME

QTY : 1

NOS

HOLD :		TYPE :		TREAT :		COST CODE :		REMARKS :								
LENGTH : 11900		WIDTH : 471		HEIGHT : 350		TOTAL S.AREA : 16.4		(M2)								
POS NO.	QTY PER ASSLY	SECTION	LENGTH	UNIT WEIGHT (Kg)	TOTAL QTY WEIGHT	GRADE	REVISION	PART ID	TREATMENT	ABRID	TOP F.S.C	PAINT & ABRID	MULTI F.S.C	ABRID	SWI NO	REMARKS
5-2-P109	1	TUB350X250X10	11576	1054***	1 1054.111	S275			MM							
5-2-P27	2	PL20*350	470	25.826	2 51.653	S275		WI								
5-2-P28	2	PL12*250	350	8.243	2 16.485	S275		WI								
5-2-P75	2	PL8*230	315	4.550	2 9.100	S275		WI								
5-2-P89	1	PL10*230	424	7.655	1 7.655	S275		WI								
5-2-P92	2	PL10*120	130	1.225	2 2.449	S275		WI								
5-2-P98	8	PL10*110	130	1.123	8 8.980	S275		WI								
5-2-P99	4	PL10*105	130	1.072	4 4.286	S275		WI								
5-2-P103	4	PL10*130	350	3.572	4 14.287	S275		WI								
5-2-P104	4	PL10*130	230	2.347	4 9.389	S275		WI								
5-2-P111	2	PL10*80.5	230	1.454	2 2.912	S275		WI								
				UNIT WEIGHT :-		1181.31										
				TOTAL WEIGHT :-		1181.31										

REV	DATE	DESCRIPTION	DRAWN	CHK'D	APPD.
BUILD'D DESC.		Tekla Corporation			
PROJECT					
CUSTOMER					
SITE LOCATION					
JOB NO.		1μÚŋŋpÁú	CAD FILES:		
DRAWING TITLE:			1μÚŋŋpÁú-5-2-A35		
FRAME SHEET 0			DRAWING NO. : 1μÚŋŋpÁú-5-2-A35		