
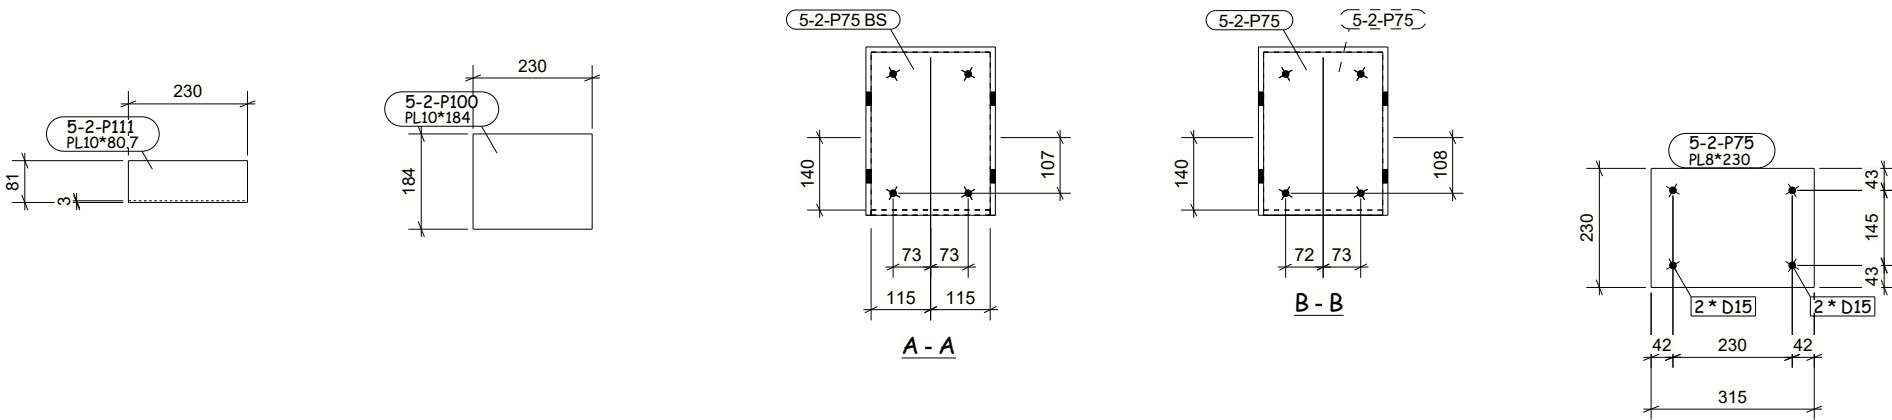


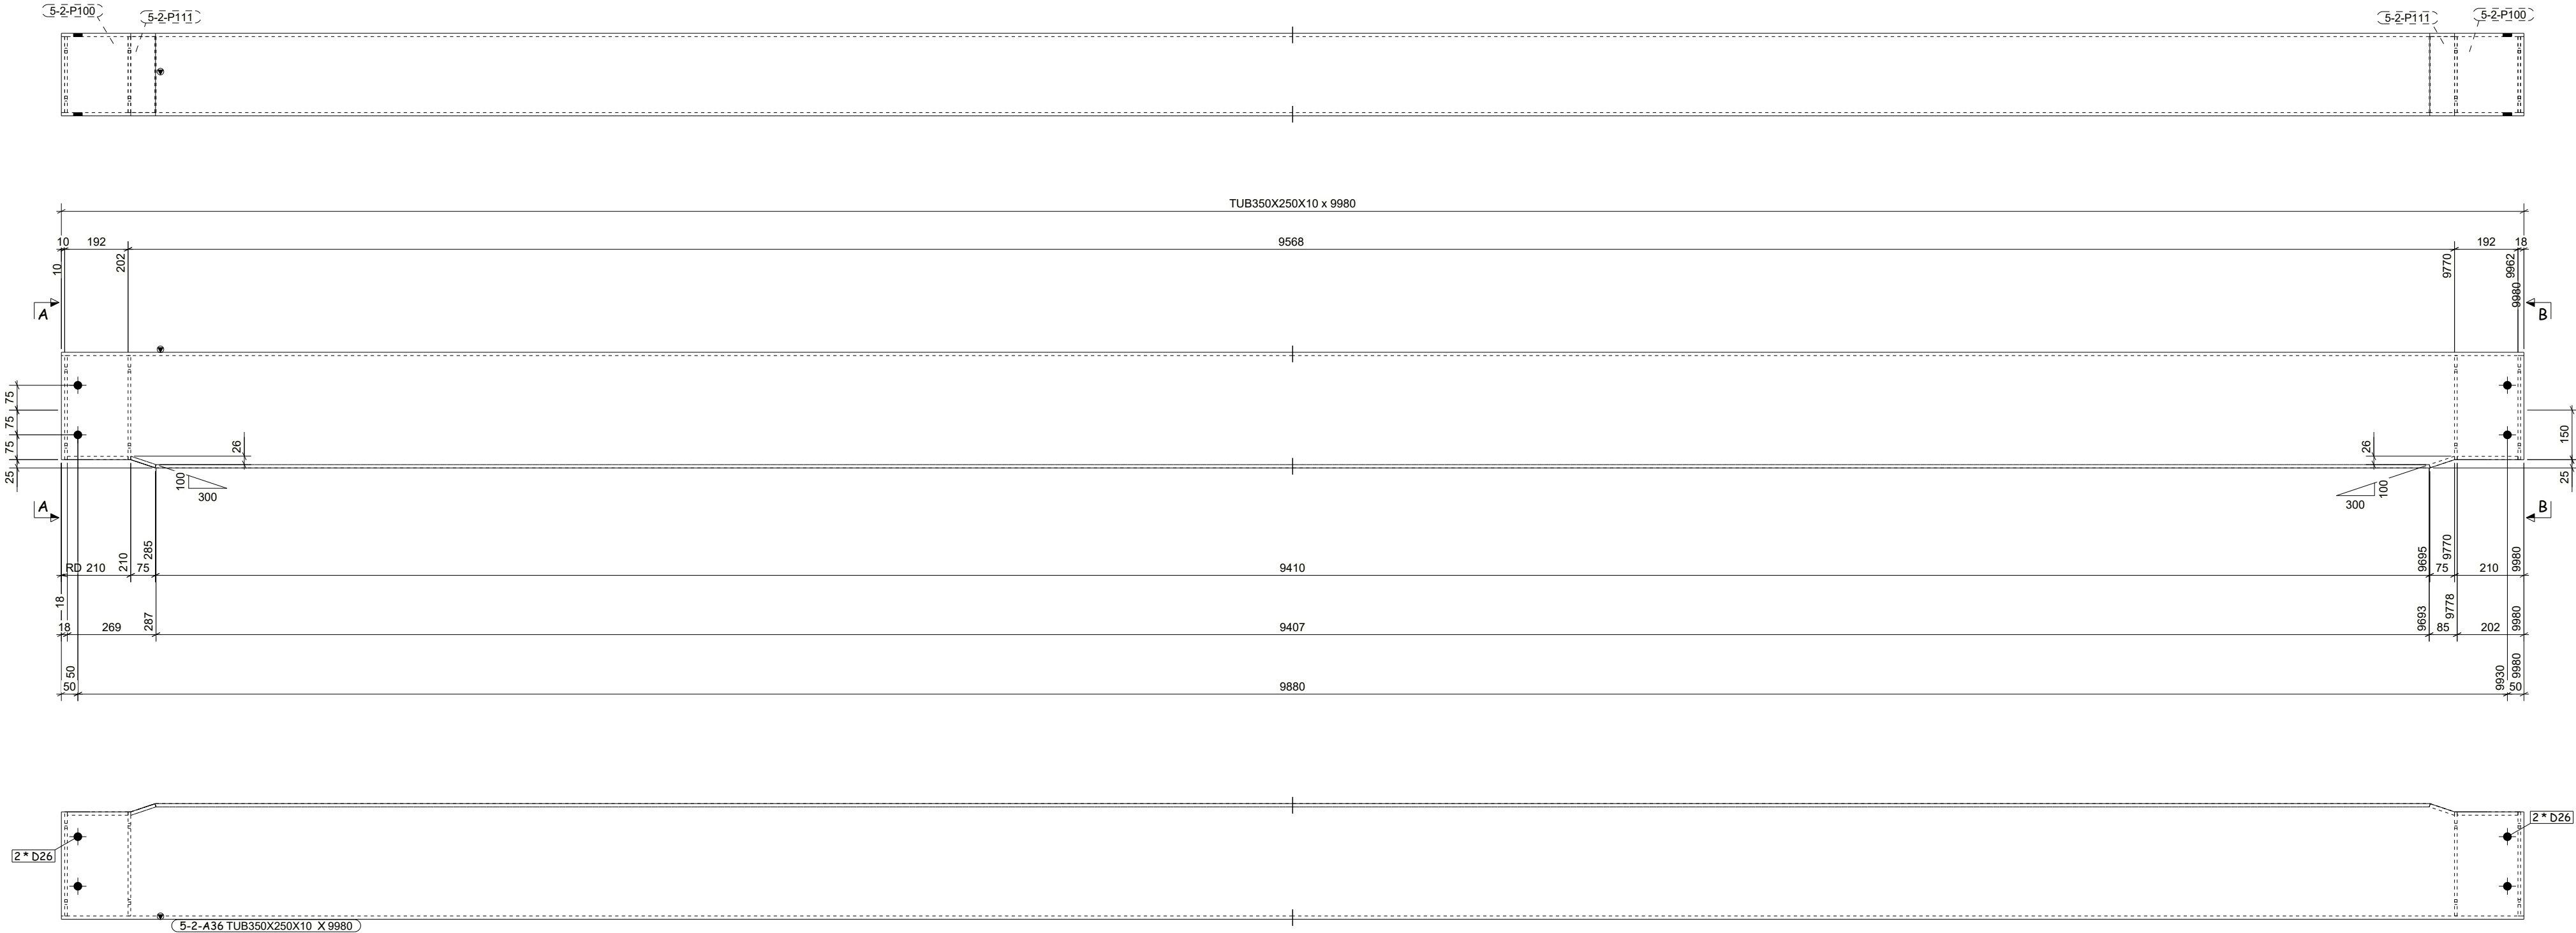

DRAWING NO. : 1μÚŋpÁú-5-2-A36										REV.:									
ERECTION MARK : 1μÚŋpÁú-5-2-A36					DESCRIPTION : BEAM					QTY: 1 NOS									
HOLD :		TYPE :		TREAT :		COST CODE :		REMARKS :											
LENGTH : 9980		WIDTH : 250		HEIGHT : 350		TOTAL S AREA :		12.7 (M2)											
POS NO.	QTY PER ASSLY	SECTION		LENGTH	UNIT WEIGHT (Kg)	TOTAL QTY	WEIGHT	GRADE	REVISION	PART	TREATMENT	ABRN ID	TOP F.S.S. ABRN ID	PARTIAL S.A. ABRN ID	MULTIPLY CC ABRN ID	SWI NO	REMARKS		
5-2-P36	1	TUB350X250X10		9980	908.779	1	908.779	S275		MM									
5-2-P75	4	PL8*230		315	4.549	4	18.198	S275		WI									
5-2-P100	2	PL10*184		230	3.322	2	6.643	S275		WI									
5-2-P111	2	PL10*80.8		230	1.458	2	2.916	S275		WI									
					UNIT WEIGHT :-		936.54												
					TOTAL WEIGHT :-		936.54												

1 NO. BEAM MKD' 1μÚŋpÁú-5-2-A36

REV	DATE	DESCRIPTION	DRAWN	CHK'D	APPD.
BUIL'D DESC.		Tekla Corporation			
PROJECT					
CUSTOMER					
SITE LOCATION					
JOB NO.		1μÚŋpÁú	CAD FILES:		
DRAWING TITLE:				1μÚŋpÁú-5-2-A36	
		BEAM SHEET 0		DRAWING NO. : 1μÚŋpÁú-5-2-A36	